



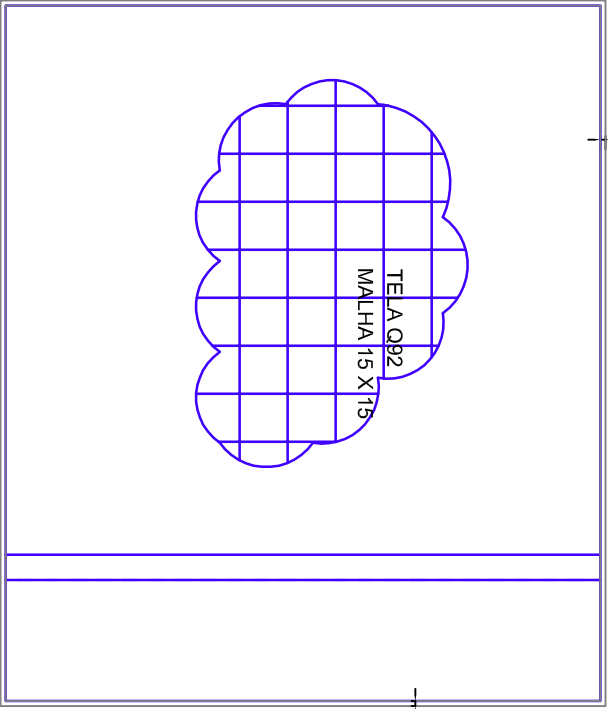


ARMADURA INFERIOR

ESC 1-75

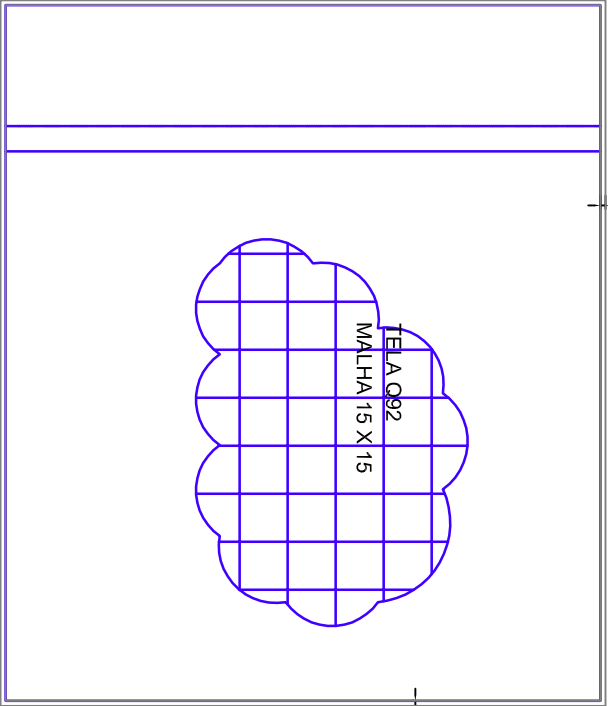


ARMADURA SUPERIOR

ESC 1-75

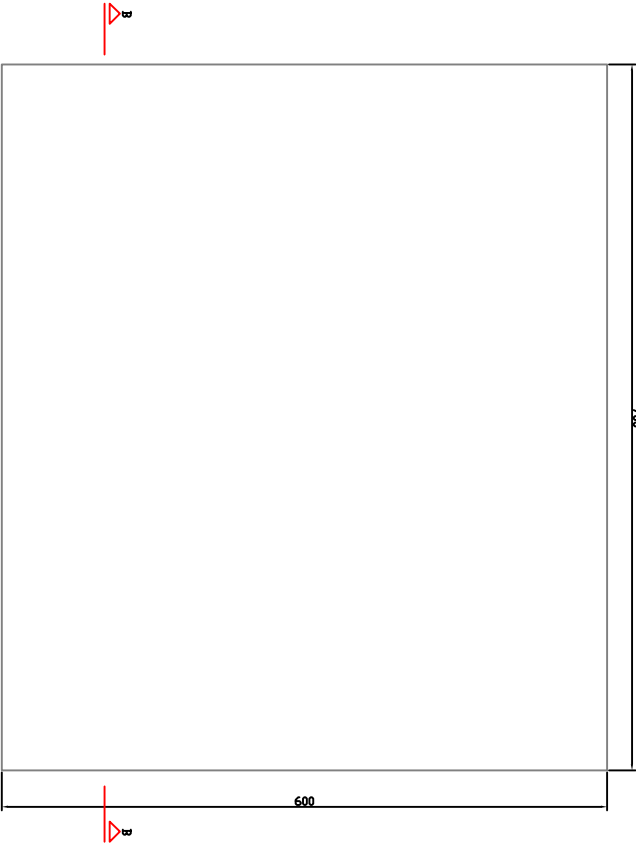


PLANTA DE FÔRMA DA BASE

ESC 1-75

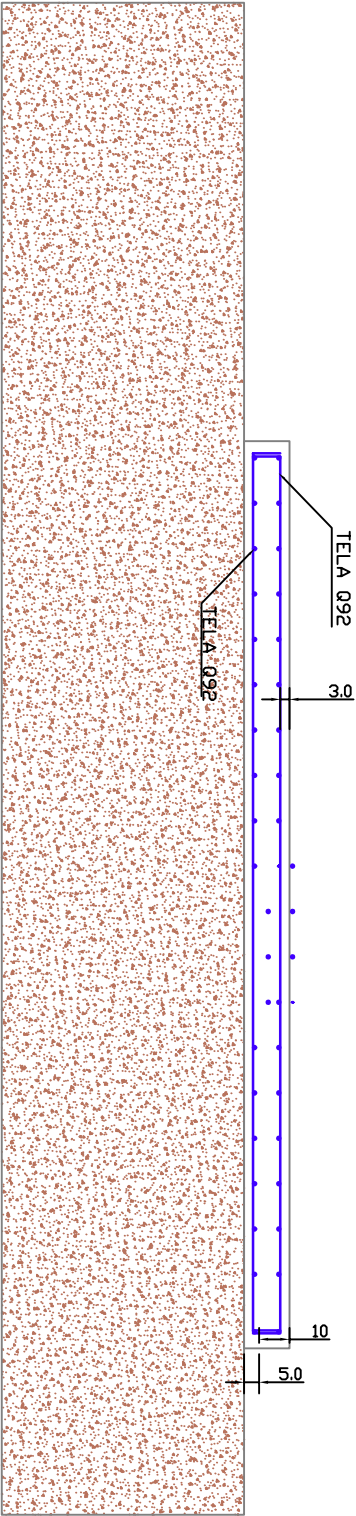

CORTE A - A

ESC 1-25

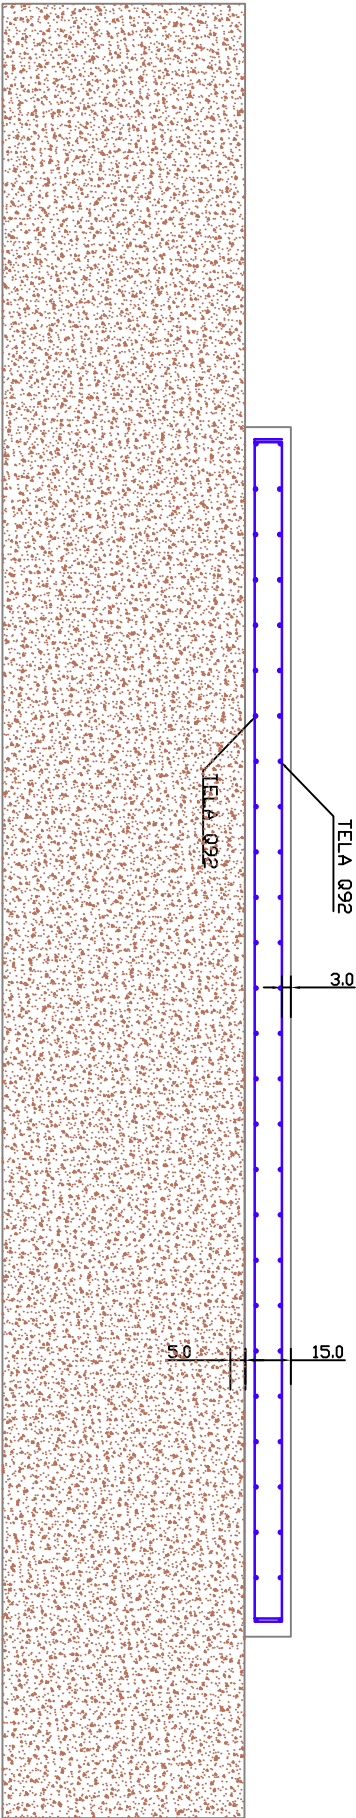

CORTE B - B

ESC 1-25

CETESB - Companhia Ambiental do Estado de São Paulo				
ARQUIVO DIGITAL:	ESTAÇÃO TELEMÉTRICA - Cubatão			
REVISÃO:	Projeto de Estrutura do Radier Vila Parisi			
FOLHA:				
001				
Projeto:	Desenho:	Escala:	Data:	Nº Desenho:
AAEM	AAEM	indicada	Ago/2022	0024-03-01/03

