



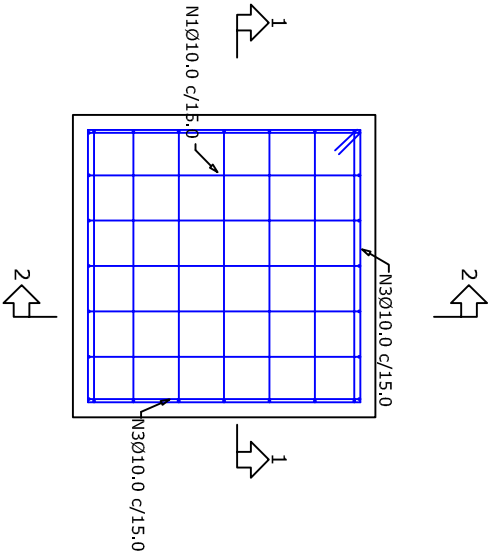


FÔRMA DO BLOCO

ESC.: 1 : 25


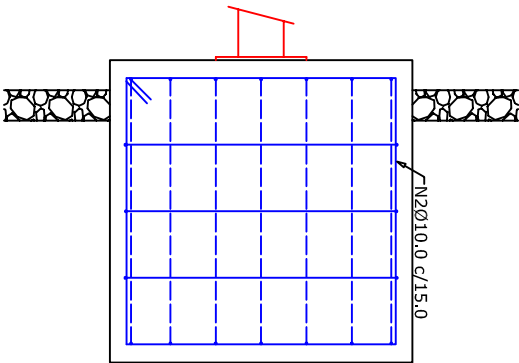


CORTE 2 - 2
ESC.: 1 : 25

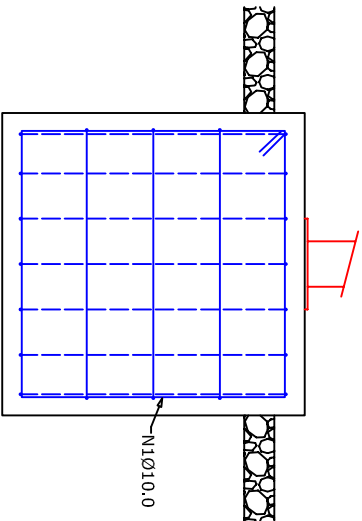


CORTE 1 - 1


ESC.: 1 : 25

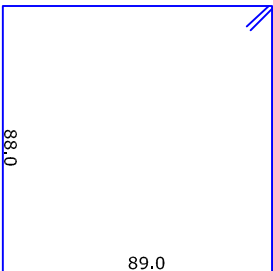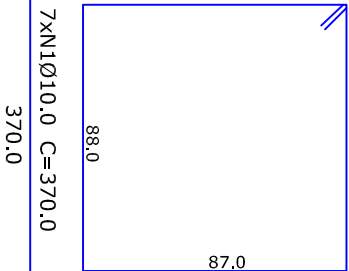


7xN2Ø10.0 C=374.0
374.0

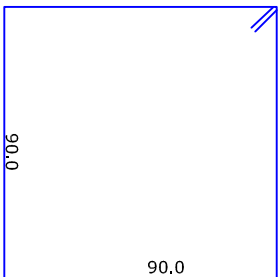

7xN3Ø10.0 C=380.0
380.0

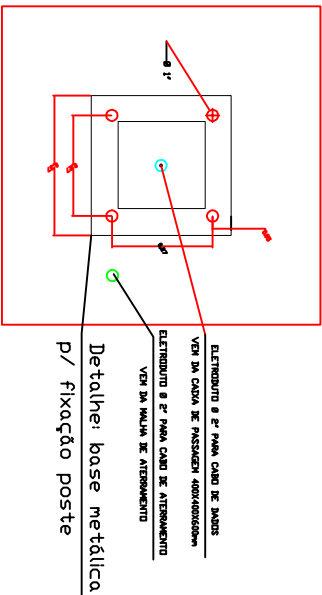


Detalhe Ancoragem bloco p/ fixação base metálica para poste
Escala 1:100

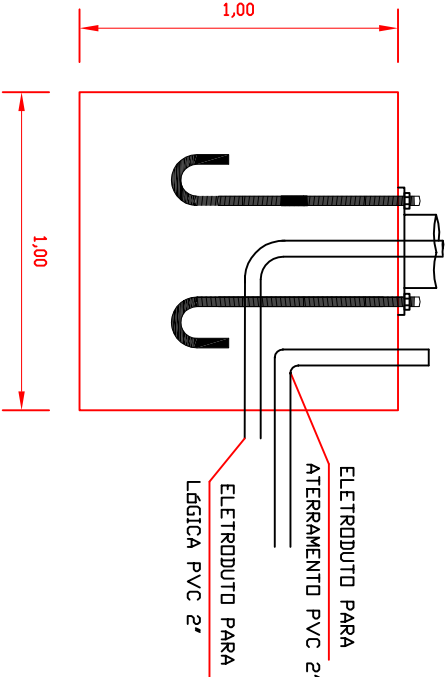

Detalhe Ancoragem bloco p/ fixação base metálica para poste
Executado apoiado sobre quatro brocas em concreto armado h=4,0m
Escala 1:100

NOTAS:

- NA MONTAGEM, OS ESTRIBOS DEVEREM FICAR COM AS COSTURAS ALTERNADAS
- MEDIDAS EM CENTÍMETROS E BITOLA EM MILÍMETROS
- CONFIRMAR MEDIDAS ANTES DA EXECUÇÃO DOS SERVIÇOS

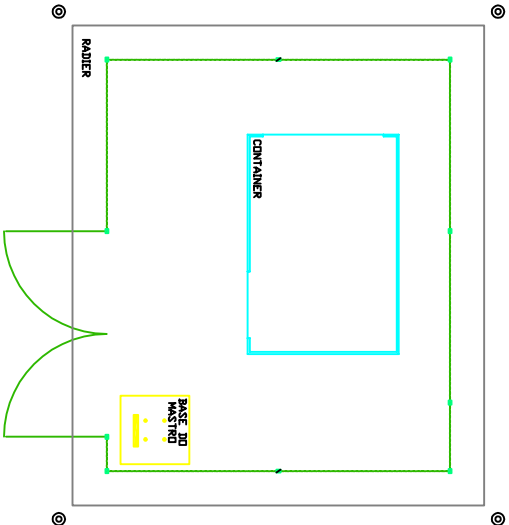

PLANTA DE LOCAÇÃO

SEM ESCALA

CETESB - Companhia Ambiental do Estado de São Paulo

ARQUIVO DIGITAL: ESTAÇÃO TELEMÉTRICA - Cubatão

REVISÃO:

FDLHA:

Projeto de Estrutura do Mastro
Vila Parisi



Projeto: AAEM

Desenho: AAEM

Escala: indicada

Data: Ago/2022

Nº Desenho: 0024-03-02/03