
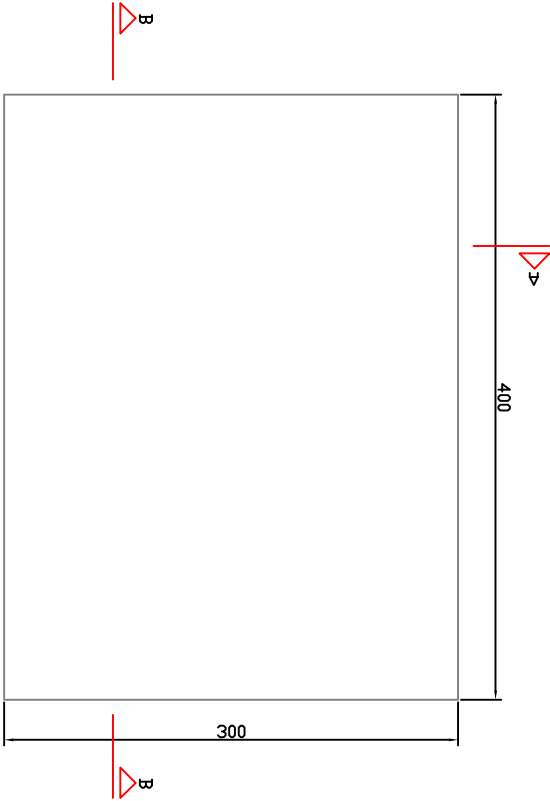
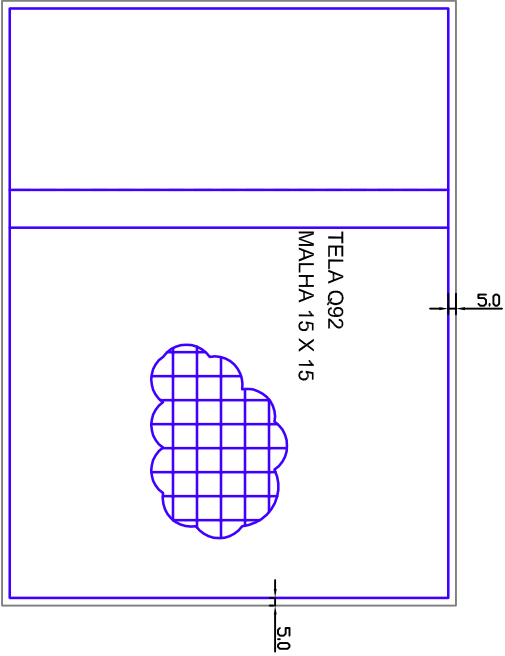


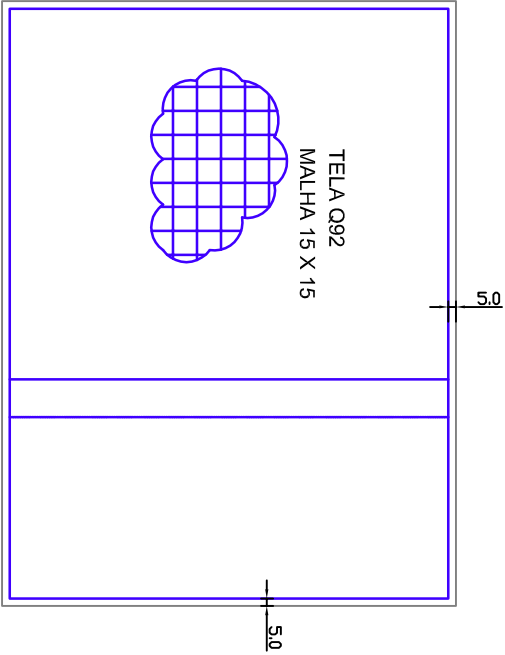

ARMADURA INFERIOR


ESC 1-50

ARMADURA SUPERIOR

ESC 1-50


PLANTA DE FÔRMA DA BASE

ESC 1-50

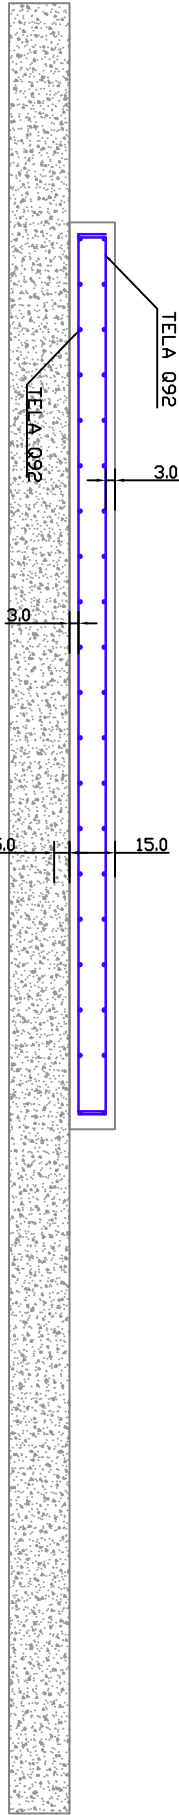

CORTE A-A

ESC 1-25

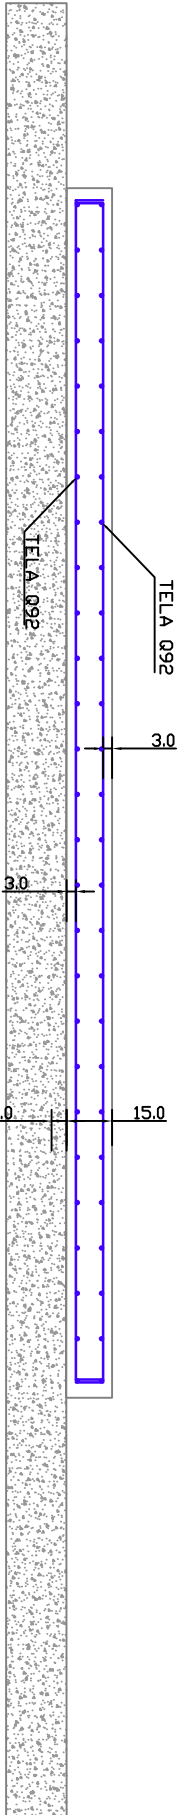

CORTE B - B

ESC 1-25

CETESB - Companhia Ambiental do Estado de São Paulo

ARQUIVO DIGITAL:		ESTAÇÃO TELEMÉTRICA - Cubatão			
REVISÃO:		Projeto de Estrutura do Radier Agência Ambiental de Cubatão			
FOLHA					
001					
Projeto:	Desenho:	Escala:	Data:		Nº Desenho
AAEM	AAEM	indicada	Ago/2022		0024-03-03/03