



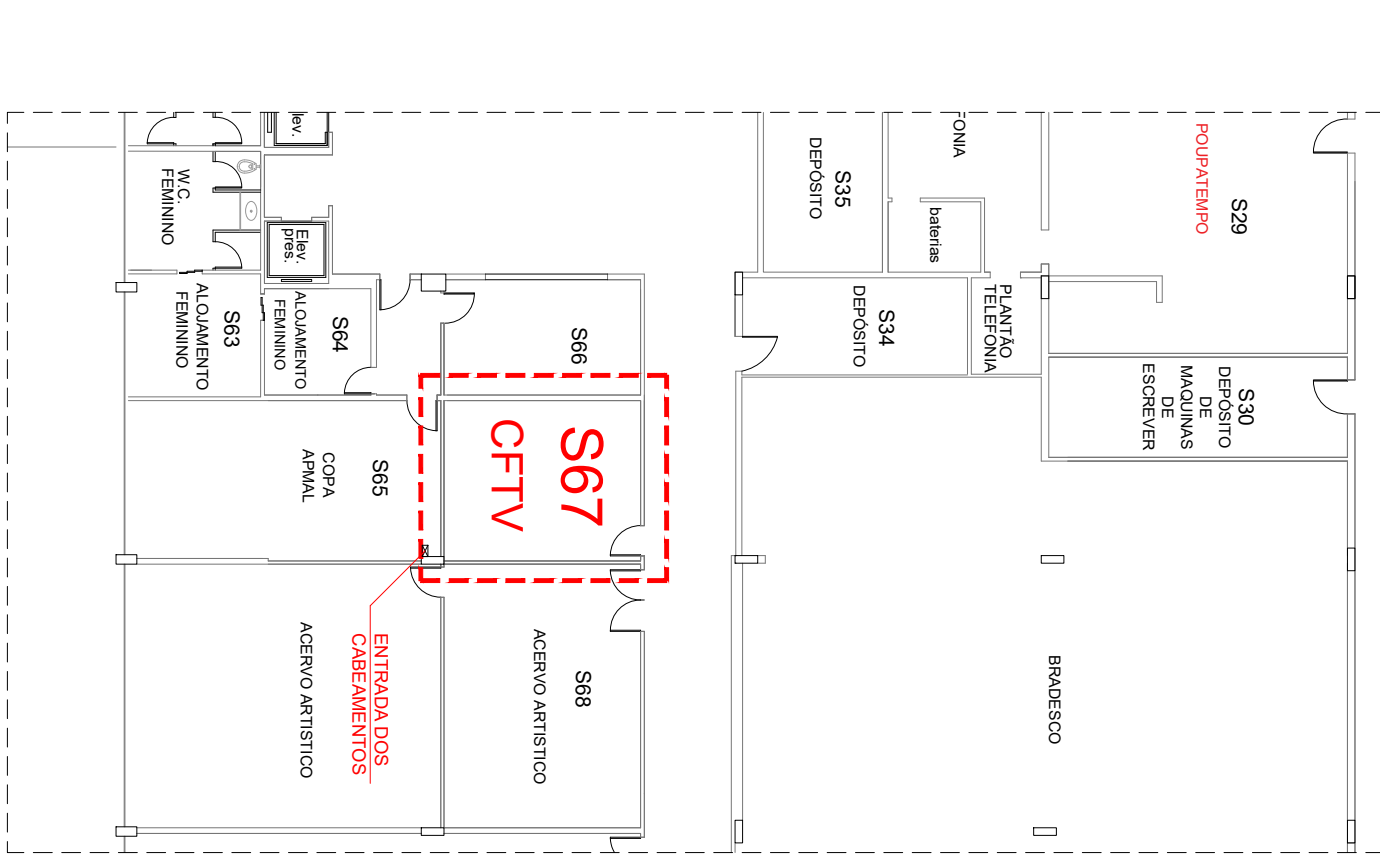


PLANTA SUBSOLO

ESCALA: 1:200

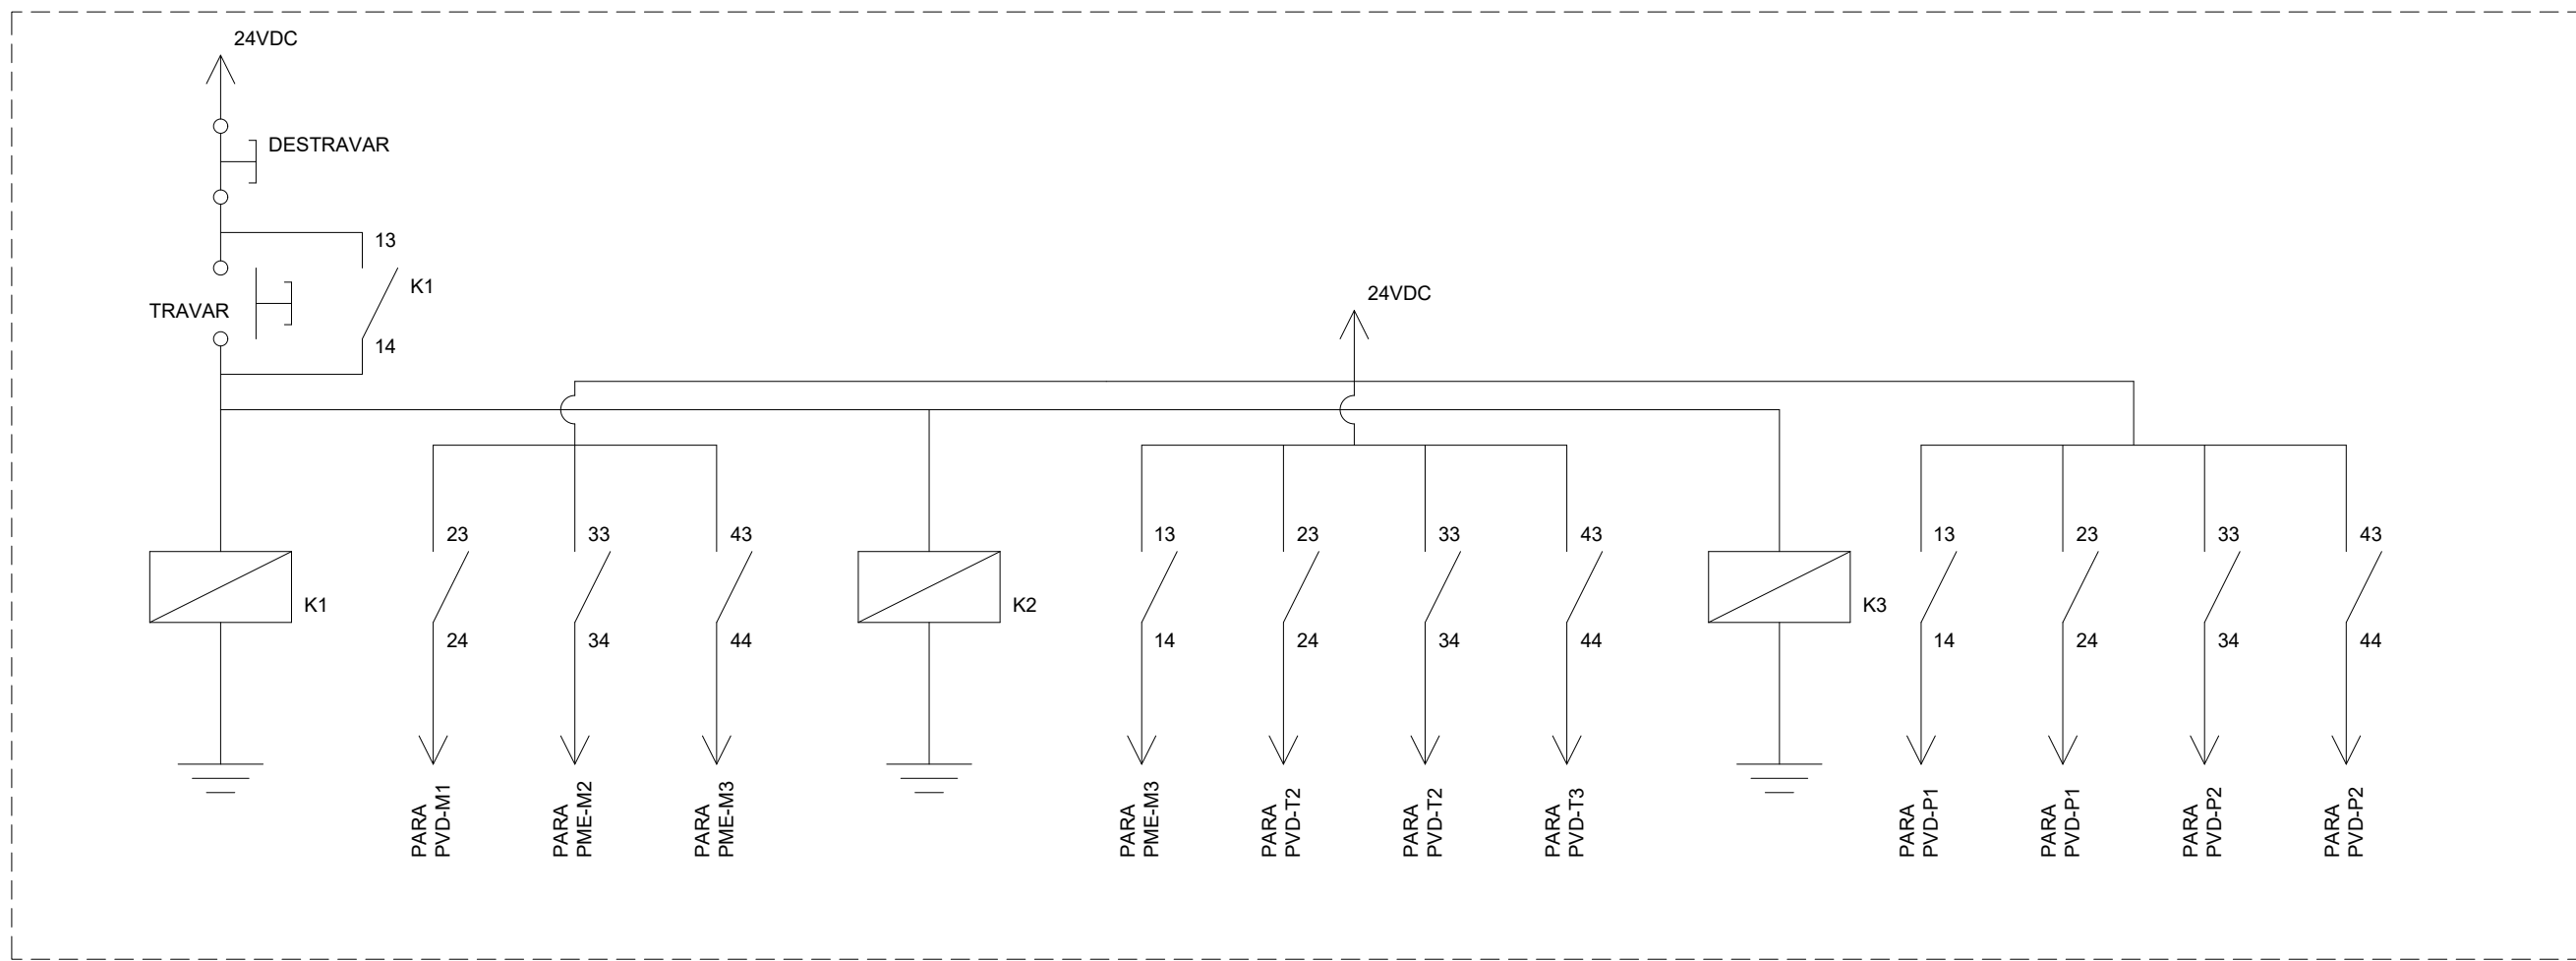


ESQUEMA DE LIGAÇÃO 24V

SEM ESCALA

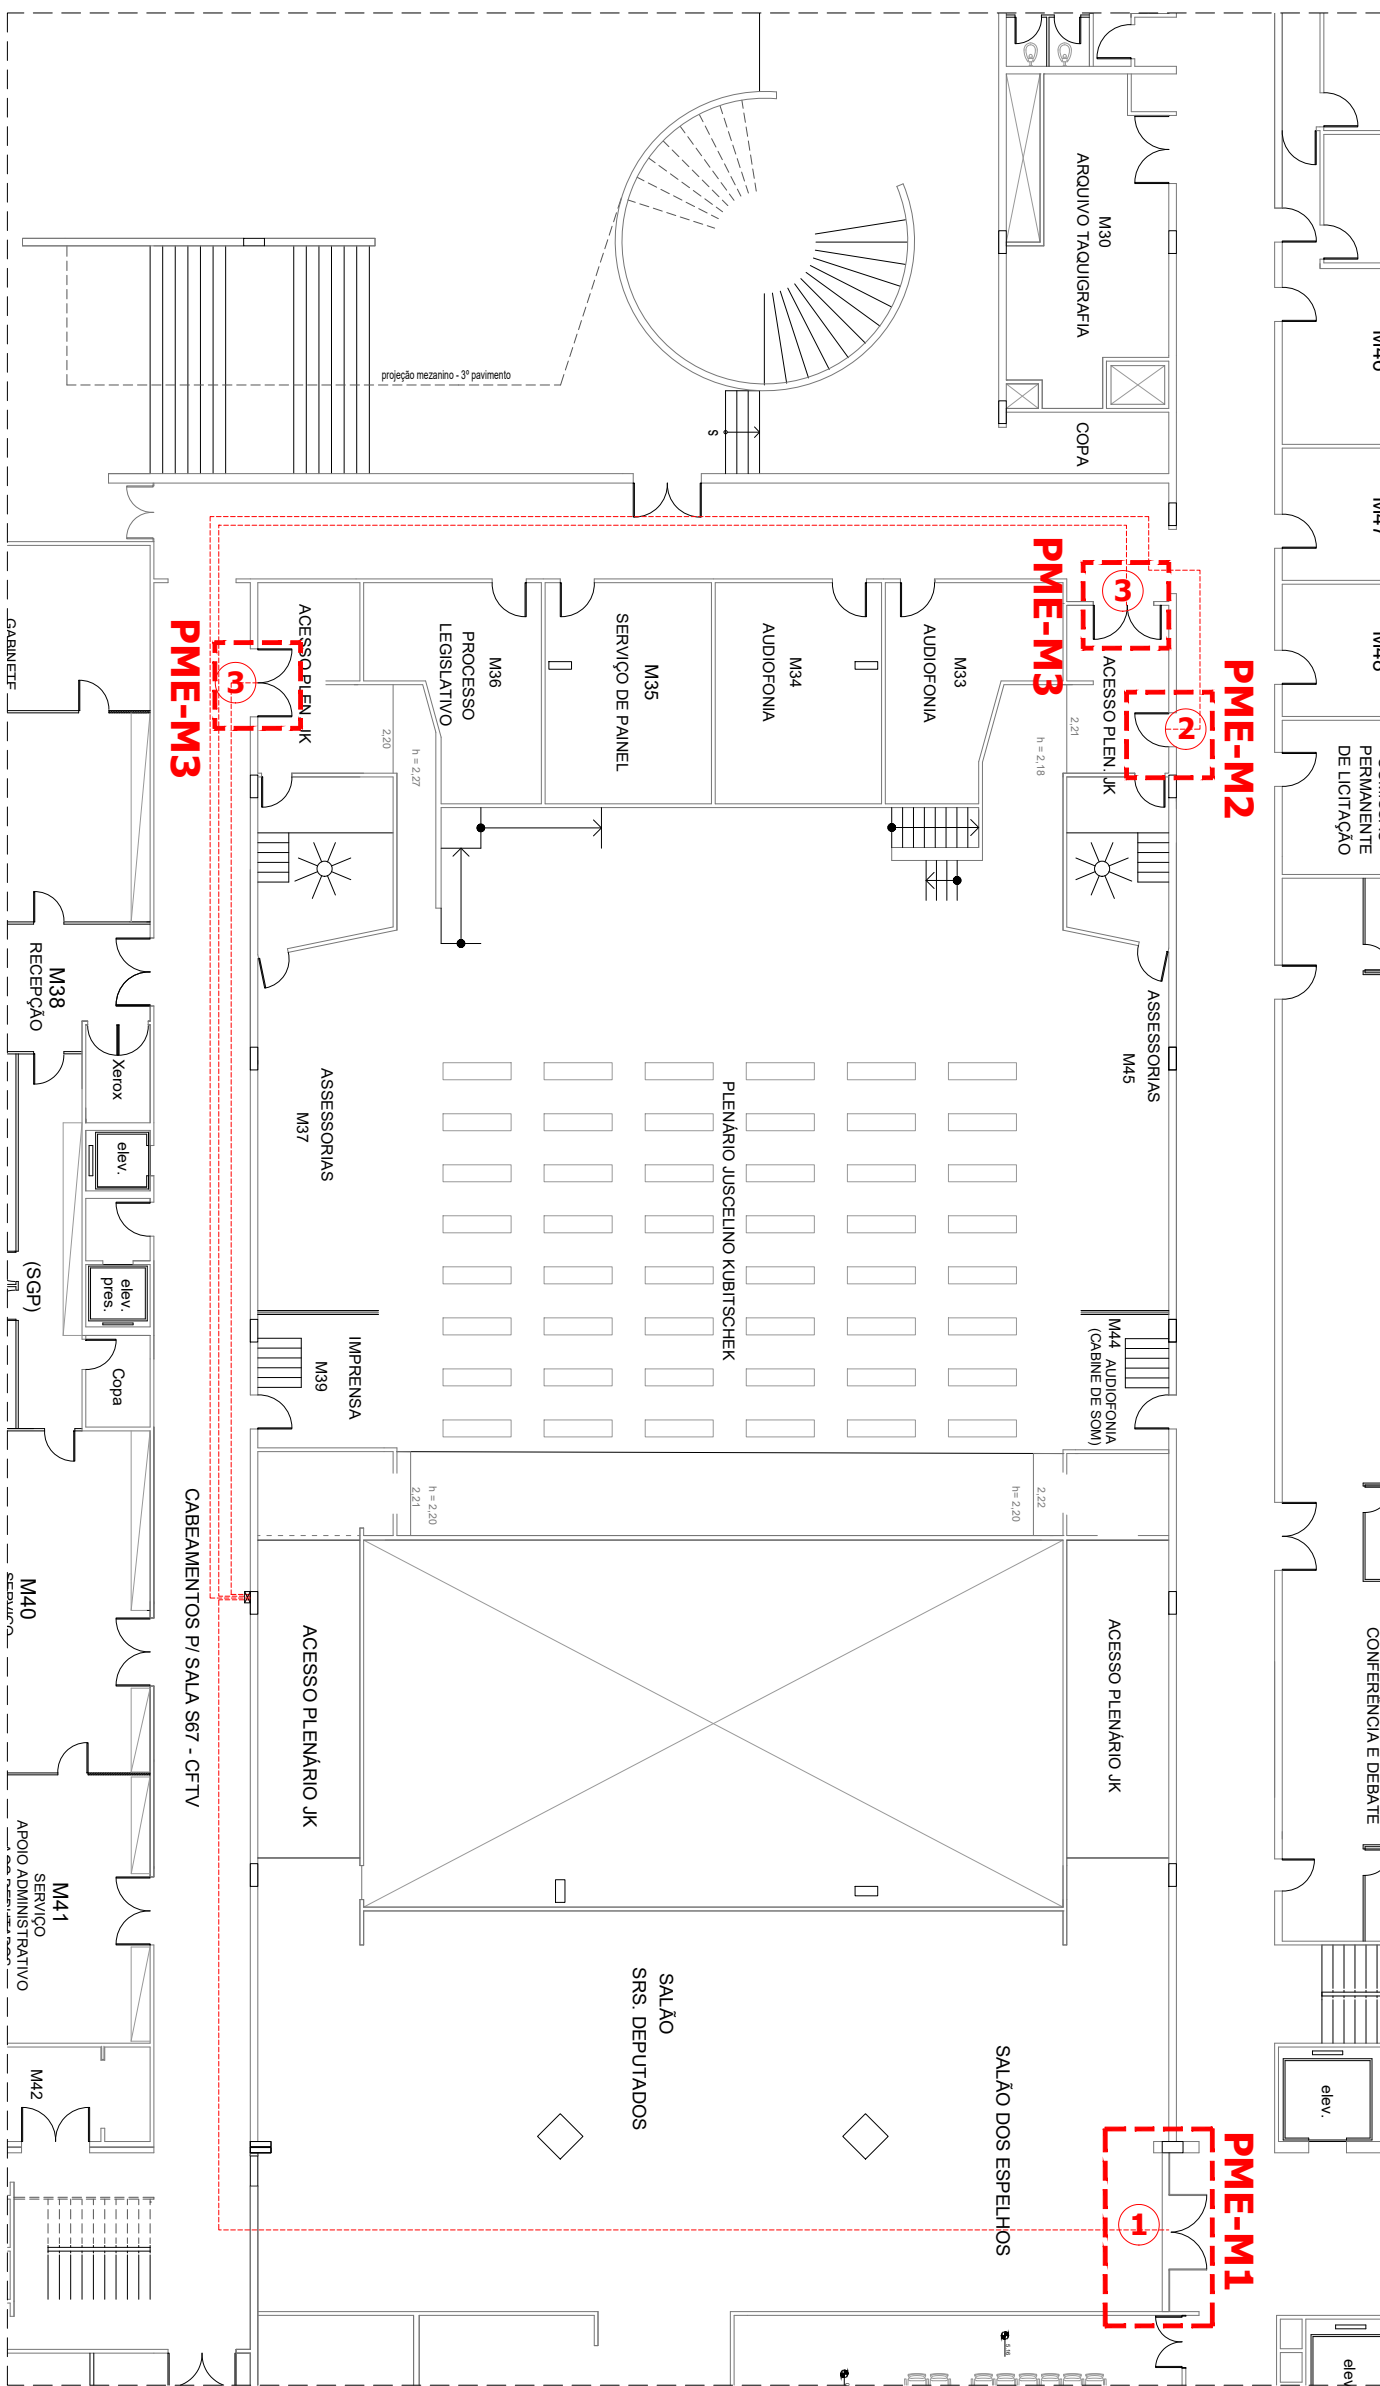


PLANTA ANDAR MONUMENTAL

ESCALA: 1:200

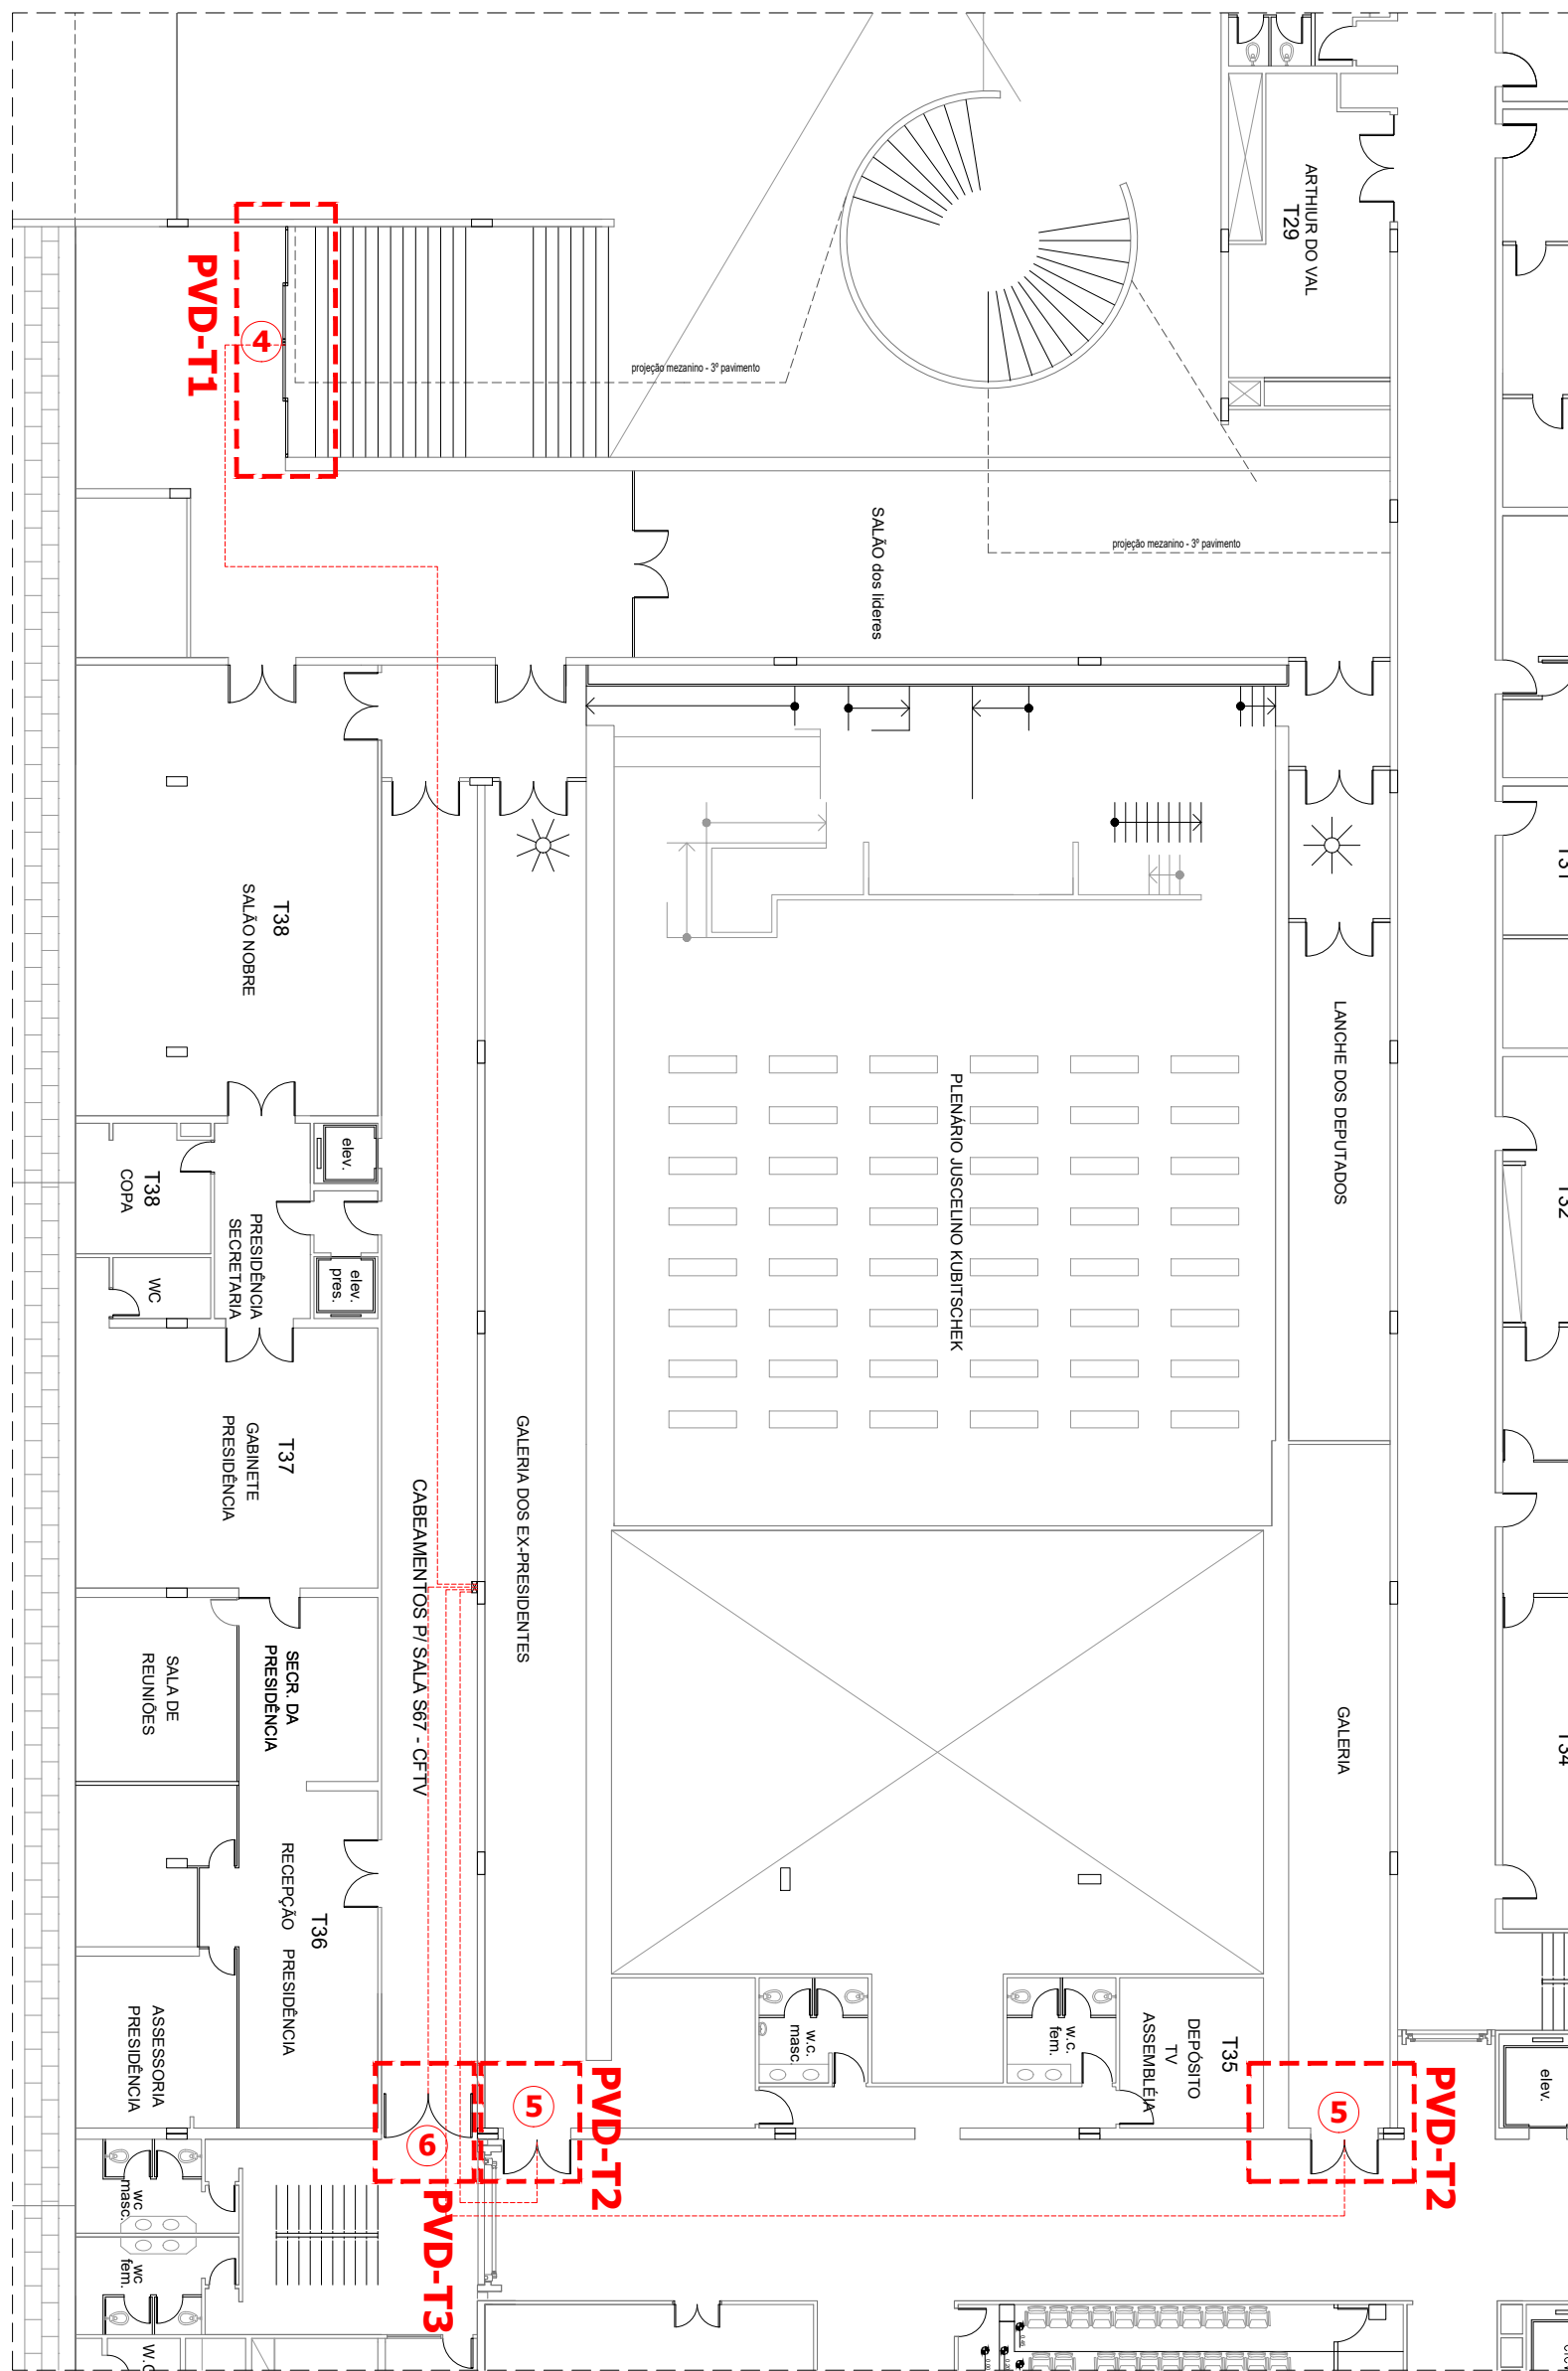

PLANTA ANDAR TERREO


ESCALA: 1:200

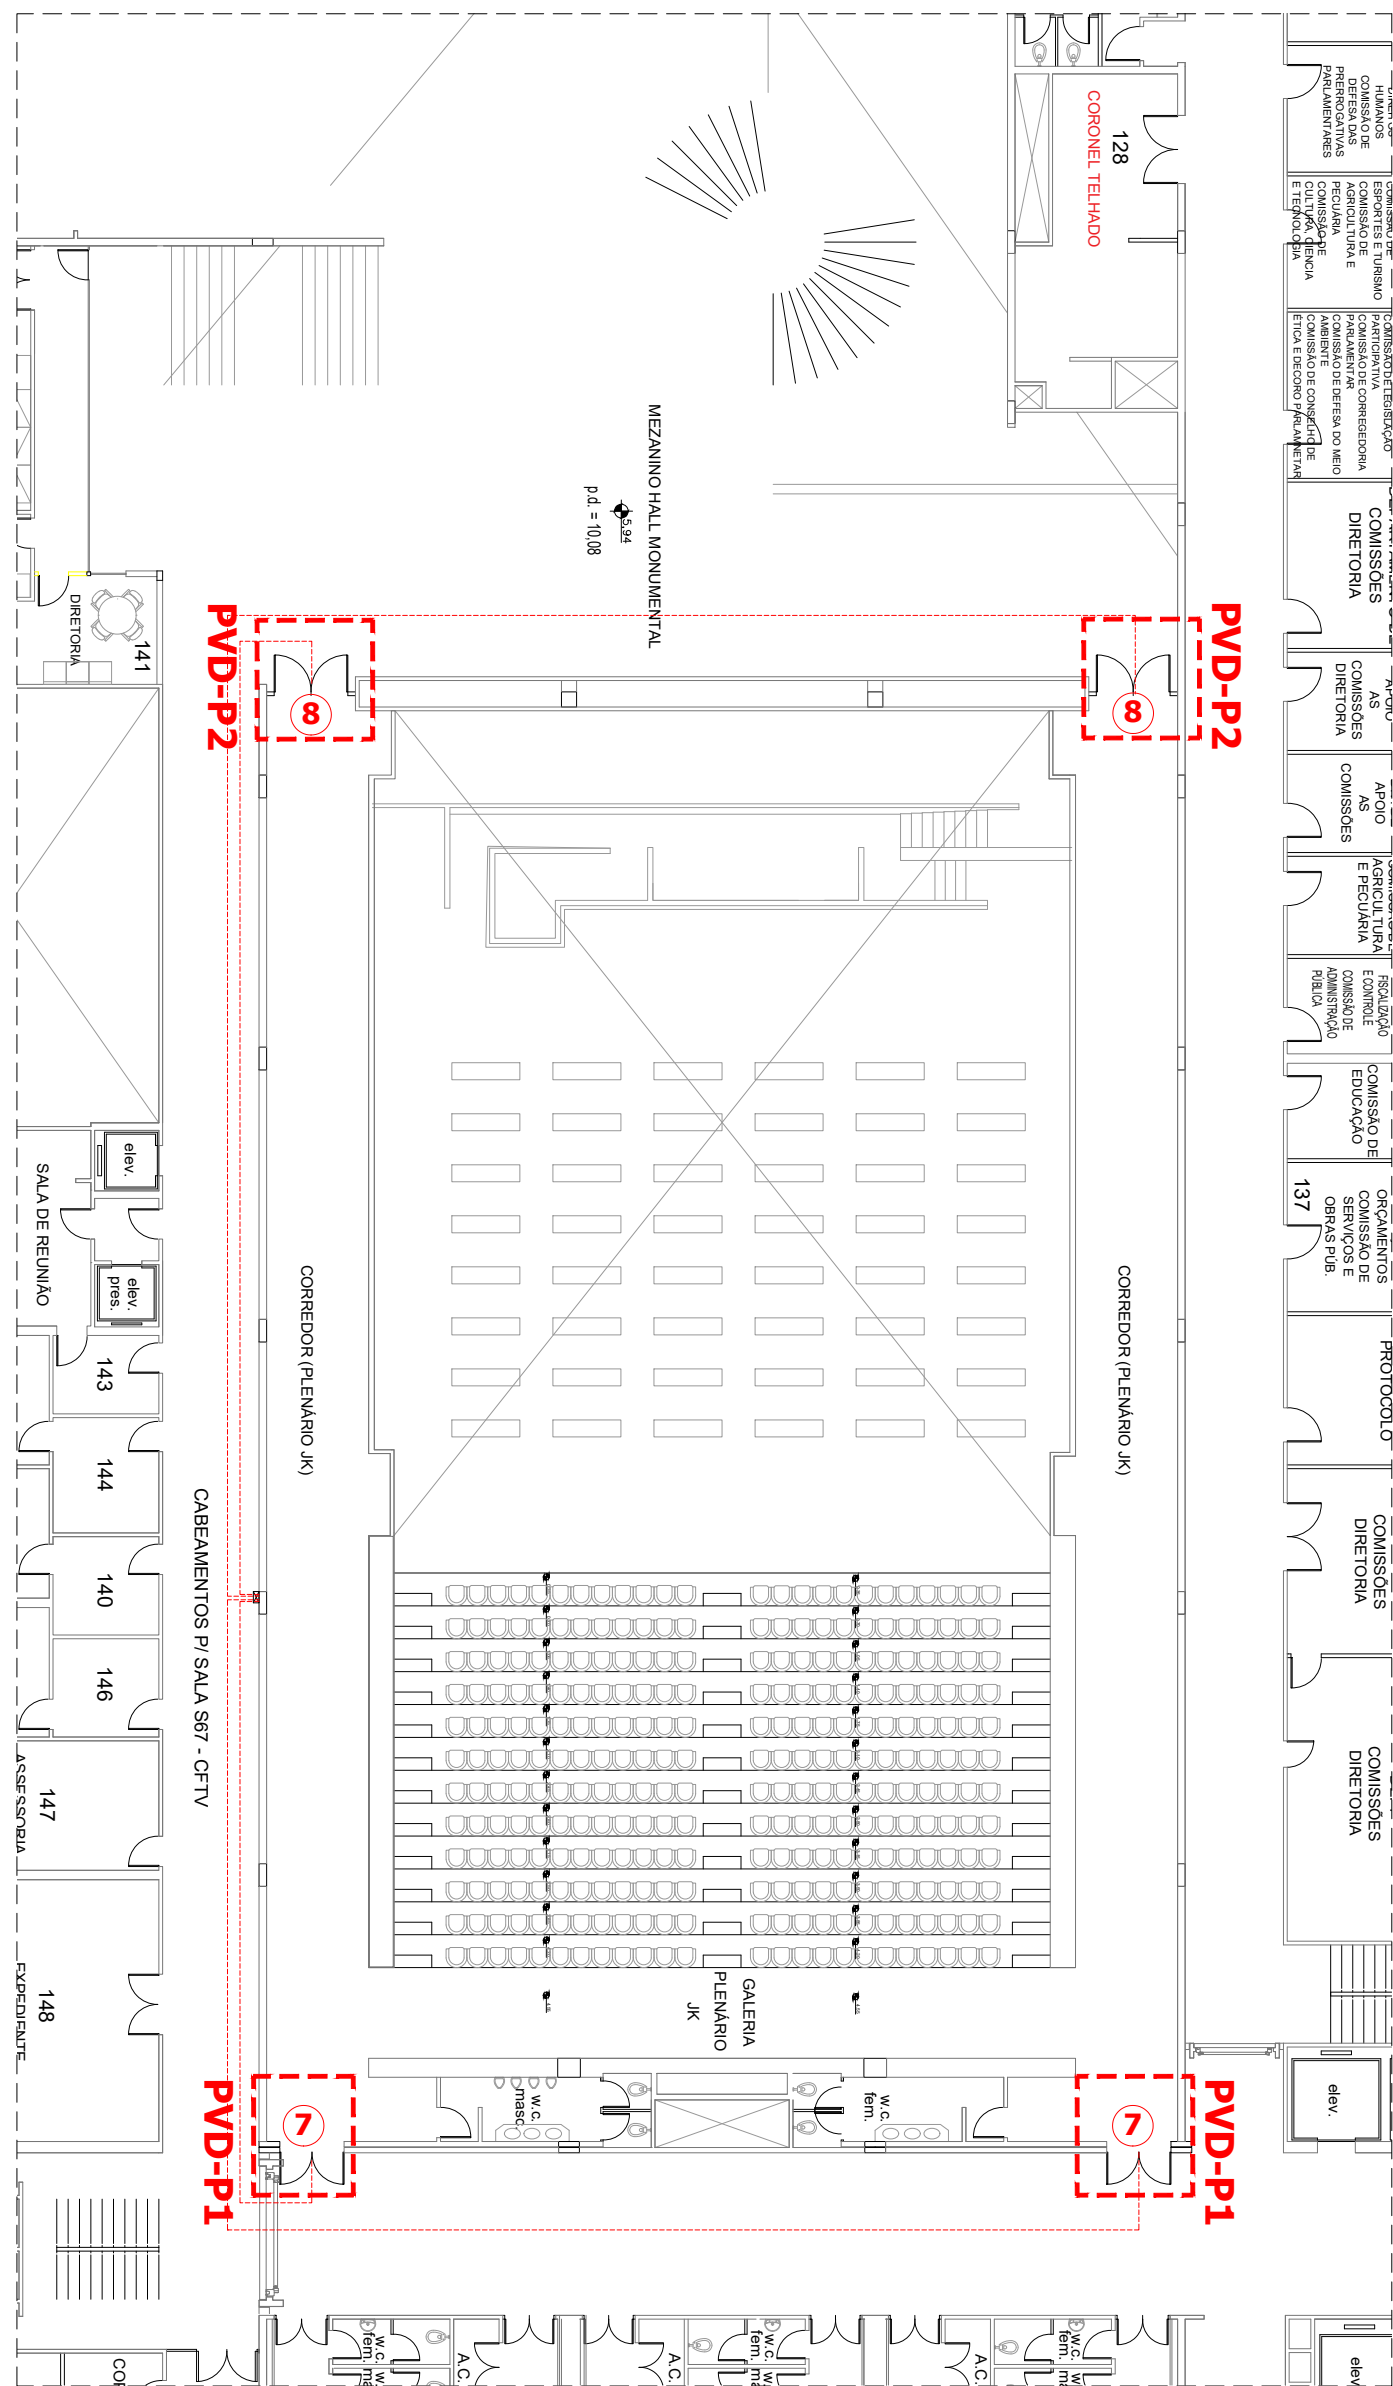

PLANTA 1.º ANDAR

ESCALA: 1:200

PLANTA CHAVE

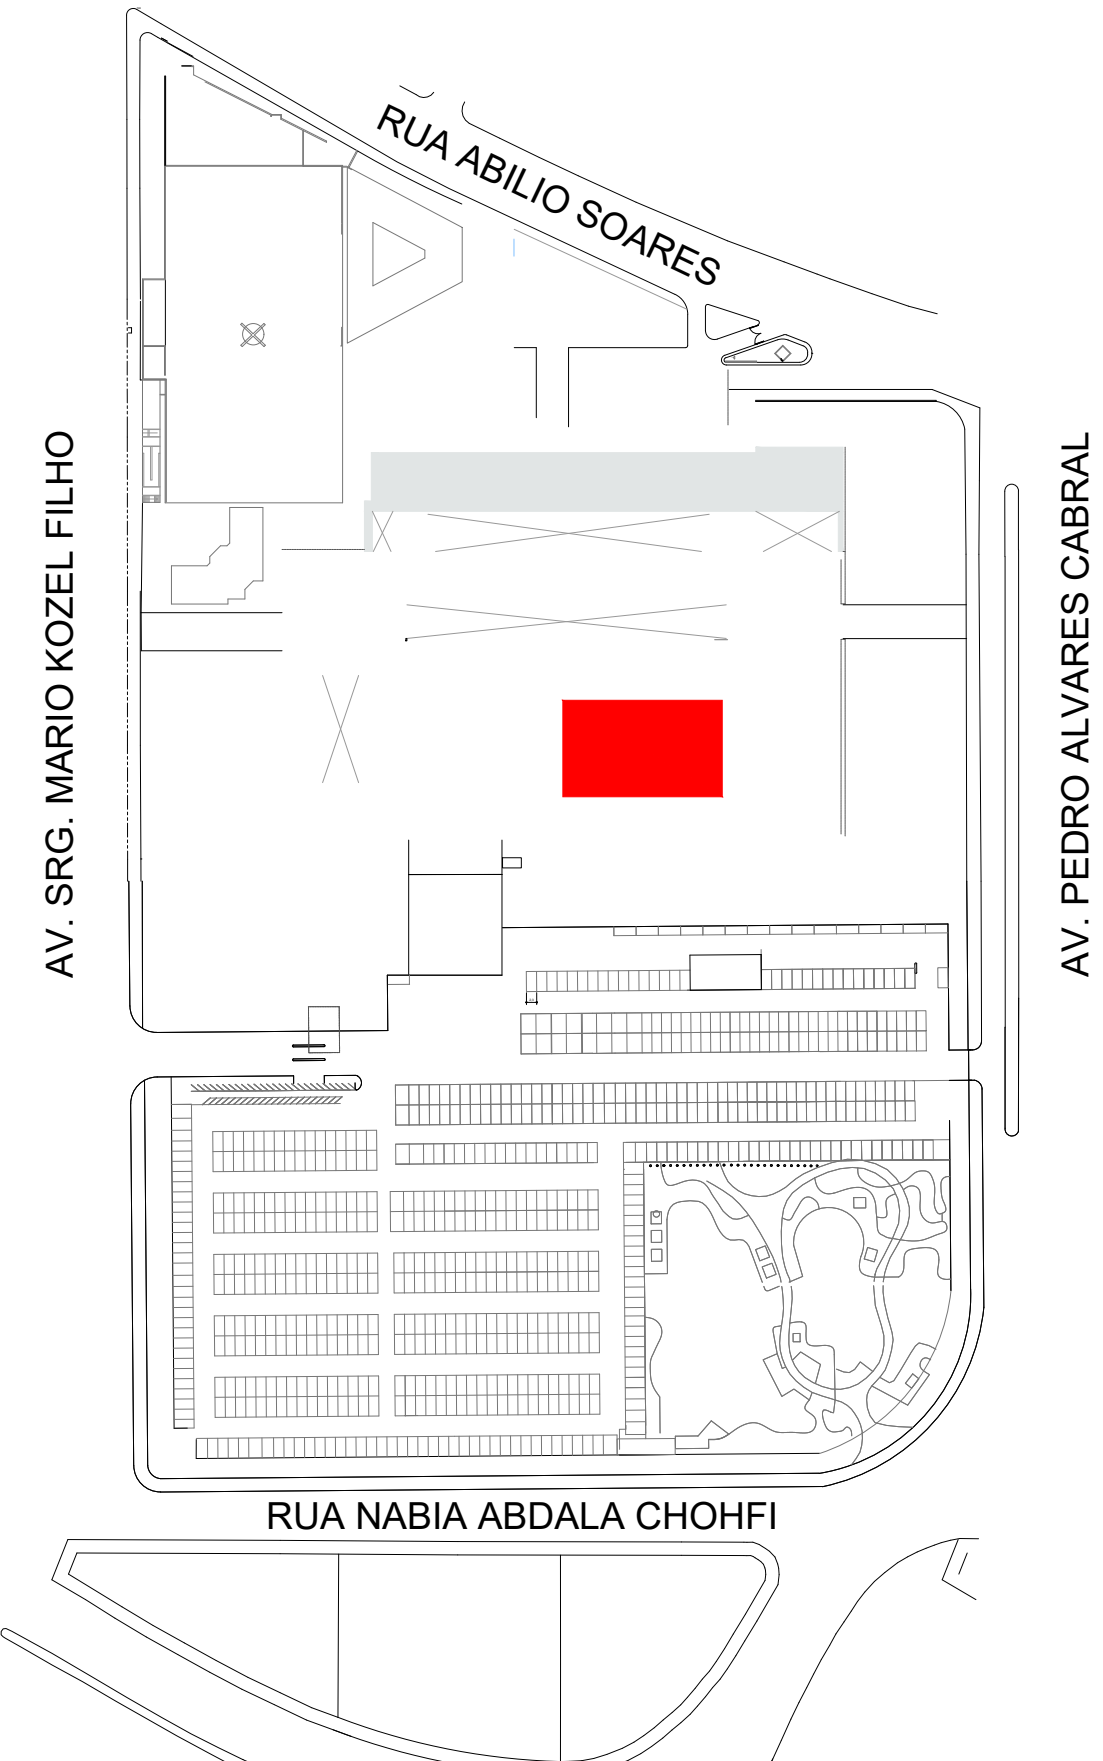

| ITEM | PAVIMENTO  | CODIGO | QT | DIMENSÕES | DESCRIÇÃO   |
|------|------------|--------|----|-----------|---|
| 1    | MONUMENTAL | PVD-M1 | 1  | 4,09X2,53 | PORTA DUPLA PIVOTANTE E DUAS PARTES FIXAS - VIDRO DE SEGURANÇA C/ BARRA ANTI-PANICO E FECHADURA MATERIAL: AÇO CARBONO ASTM 36 - 2mm ACABAMENTO INOX ESCOVADO E VIDRO TEMPERADO E LAMINADO 12mm (6mm + PVB + 6mm)                           |
| 2    | MONUMENTAL | PME-M2 | 1  | 0,9X2,53  | PORTA DE SEGURANÇA SIMPLES DE GIRO MATERIAL: CHAPA DE AÇO CARBONO ASTM 36 - 2mm - PINTADO COR PRETA   |
| 3    | MONUMENTAL | PME-M3 | 2  | 1,8X2,53  | PORTA DE SEGURANÇA DUPLA DE GIRO MATERIAL: CHAPA DE AÇO CARBONO ASTM 36 - 2mm - PINTADO COR PRETA   |
| 4    | TERREO     | PVD-T1 | 1  | 6,14X2,53 | PORTA DESLIZANTE (DUAS FOLHAS MÓVEIS E DUAS FOLHAS FIXAS) DE VIDRO DE SEGURANÇA C/ MOTOR E CREMALHEIRA ACONIAMENTO REMOTO MATERIAL: AÇO CARBONO ASTM 36 - 2mm ACABAMENTO INOX ESCOVADO E VIDRO TEMPERADO E LAMINADO 12mm (6mm + PVB + 6mm) |
| 5    | TERREO     | PVD-T2 | 2  | 1,8X2,53  | PORTA DUPLA PIVOTANTE - VIDRO DE SEGURANÇA C/ BARRA ANTI-PANICO E FECHADURA MATERIAL: AÇO CARBONO ASTM 36 - 2mm ACABAMENTO INOX ESCOVADO E VIDRO TEMPERADO E LAMINADO 12mm (6mm + PVB + 6mm)                                               |
| 6    | TERREO     | PVD-T3 | 1  | 2,4X2,53  | PORTA DUPLA PIVOTANTE - VIDRO DE SEGURANÇA C/ BARRA ANTI-PANICO E FECHADURA MATERIAL: AÇO CARBONO ASTM 36 - 2mm ACABAMENTO INOX ESCOVADO E VIDRO TEMPERADO E LAMINADO 12mm (6mm + PVB + 6mm)                                               |
| 7    | 1.PAV      | PVD-P1 | 2  | 1,6X2,53  | PORTA DUPLA PIVOTANTE - VIDRO DE SEGURANÇA C/ BARRA ANTI-PANICO E FECHADURA MATERIAL: AÇO CARBONO ASTM 36 - 2mm ACABAMENTO INOX ESCOVADO E VIDRO TEMPERADO E LAMINADO 12mm (6mm + PVB + 6mm)                                               |
| 8    | 1.PAV      | PVD-P2 | 2  | 2,4X2,53  | PORTA DUPLA PIVOTANTE - VIDRO DE SEGURANÇA C/ BARRA ANTI-PANICO E FECHADURA MATERIAL: AÇO CARBONO ASTM 36 - 2mm ACABAMENTO INOX ESCOVADO E VIDRO TEMPERADO E LAMINADO 12mm (6mm + PVB + 6mm)                                               |

NOTA: CONFERIR MEDIDAS NA OBRA

NOTA: DIMENSÕES DO VÃO TOTAL

ATENDER AS NORMAS:

NBR 7199 - VIDROS NA CONSTRUÇÃO CIVIL

NBR 14697 - VIDRO LAMINADO

NBR 8800 - CÁLCULO E EXECUÇÃO DE ESTRUTURAS DE AÇO

NBR 6123 - FORÇAS DEVIDAS AO VENTO EM EDIFICAÇÕES

NBR 6120 - CARGAS PARA CALCULO DE ESTRUTURA EM EDIFICAÇÕES











AISC - AMERICAN INSTITUTE OF STEEL CONSTRUCTIONS

AWS - AMERICAN WELDING SOCIETY AISI - AMERICAN IRON AND STEEL INSTITUTE.

OBSERVAÇÕES

1- AS FECHADURAS MAGNÉTICAS SERÃO CONTROLADAS PELA CENTRAL DE CFTV SALA S67 SUBSOLO



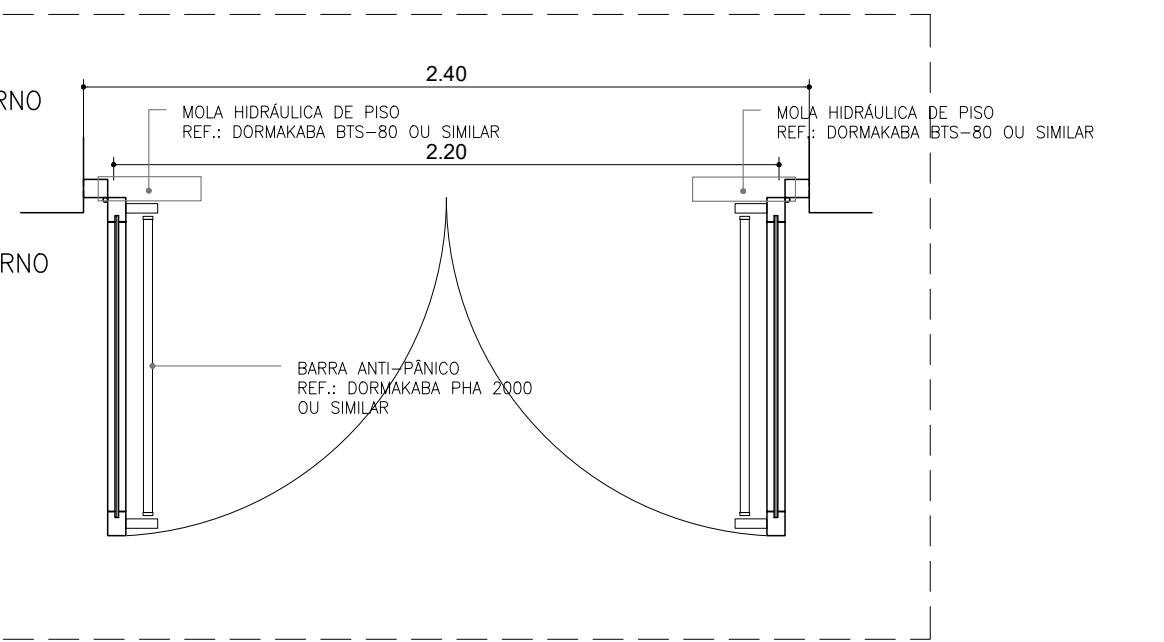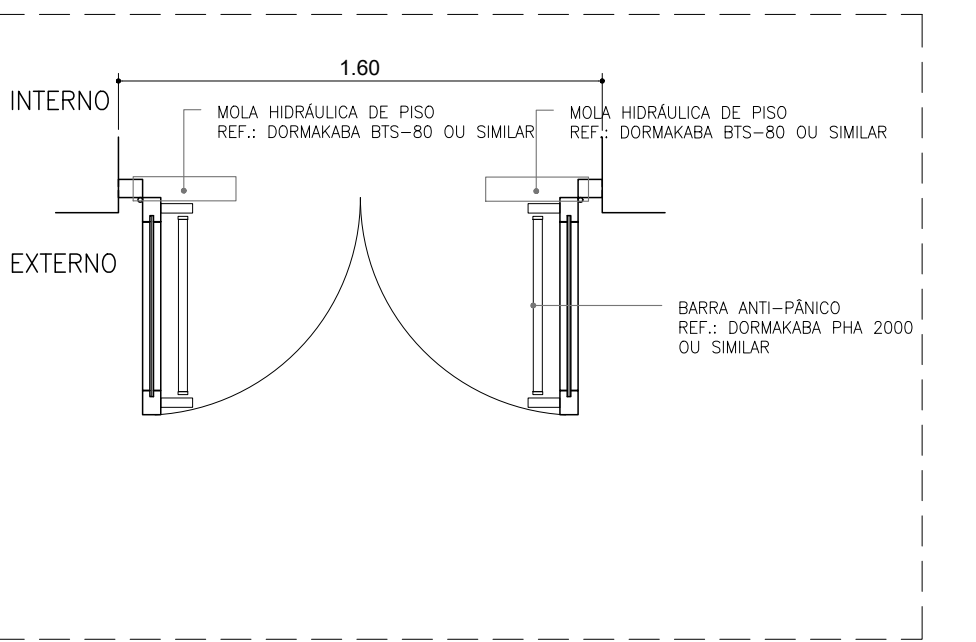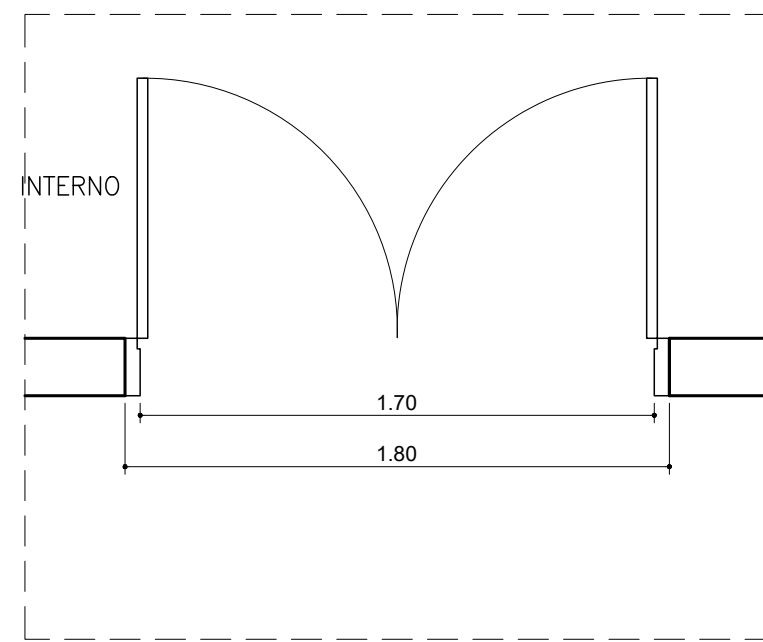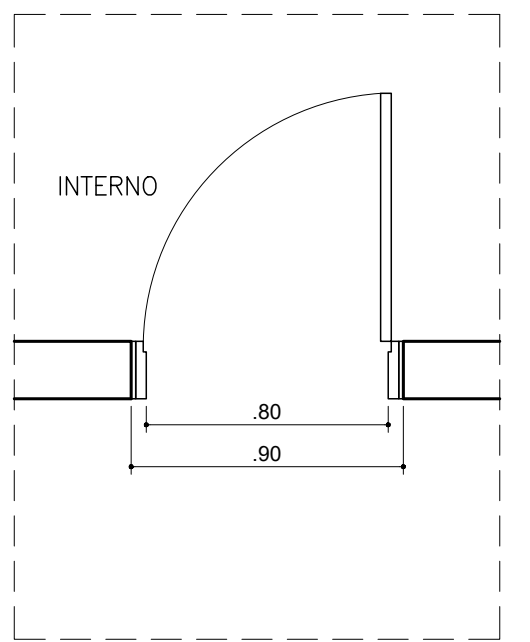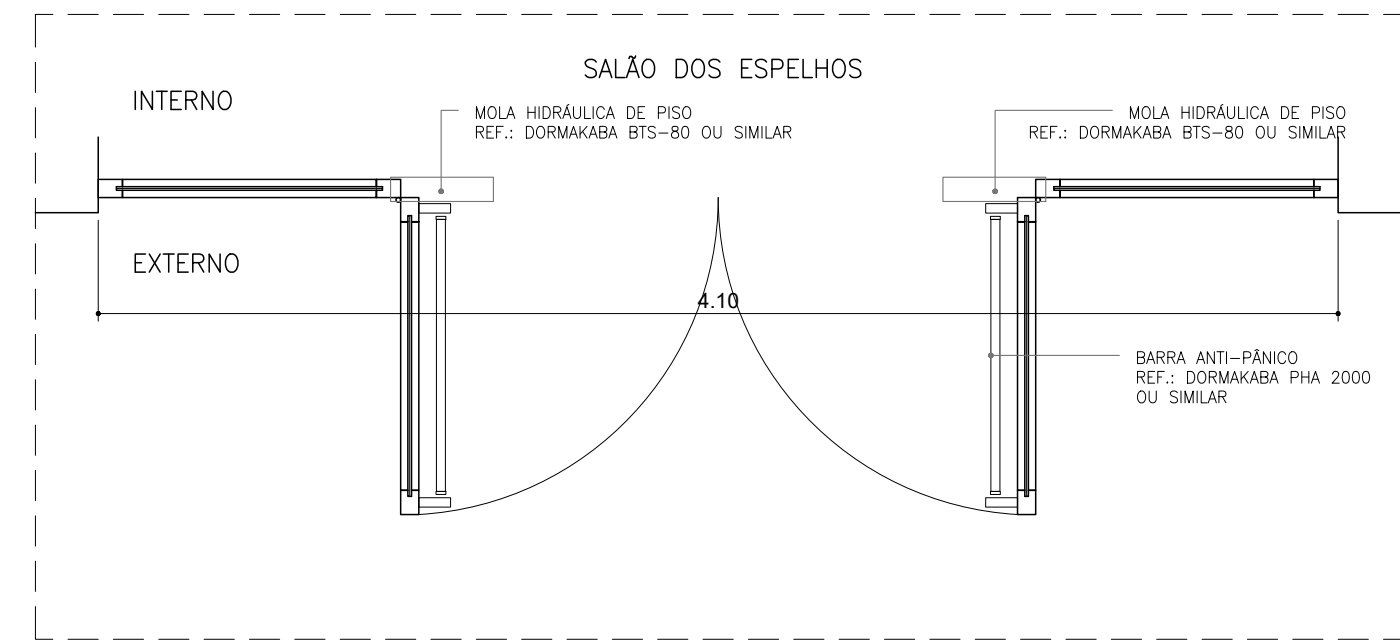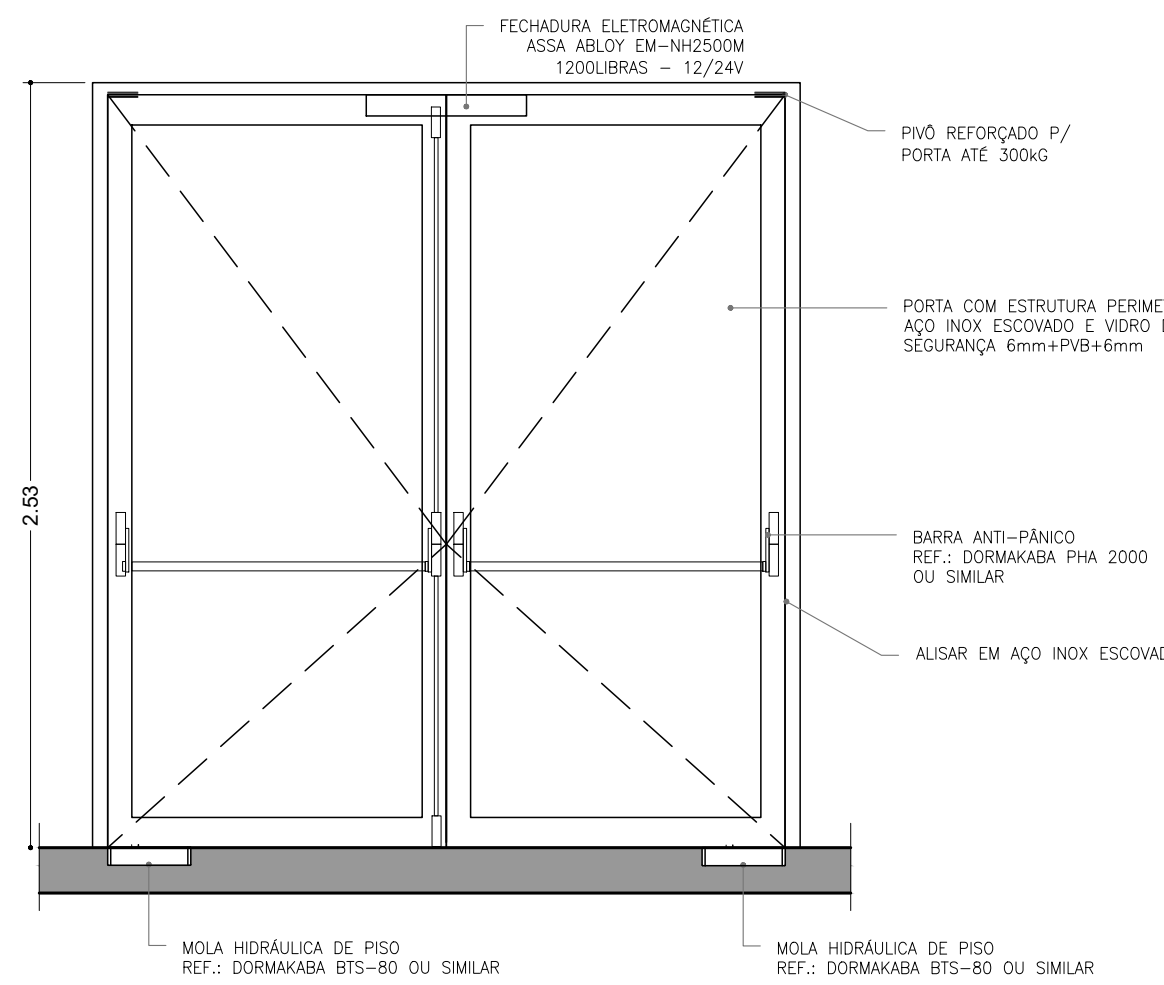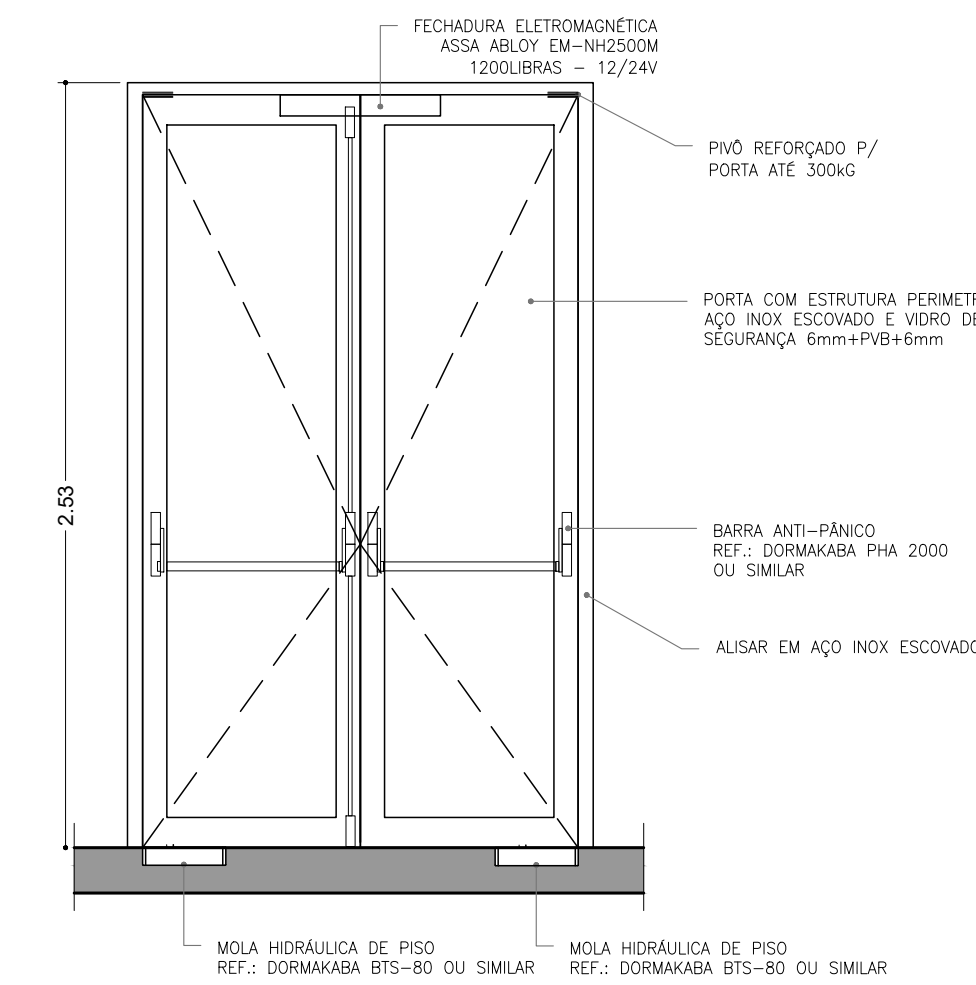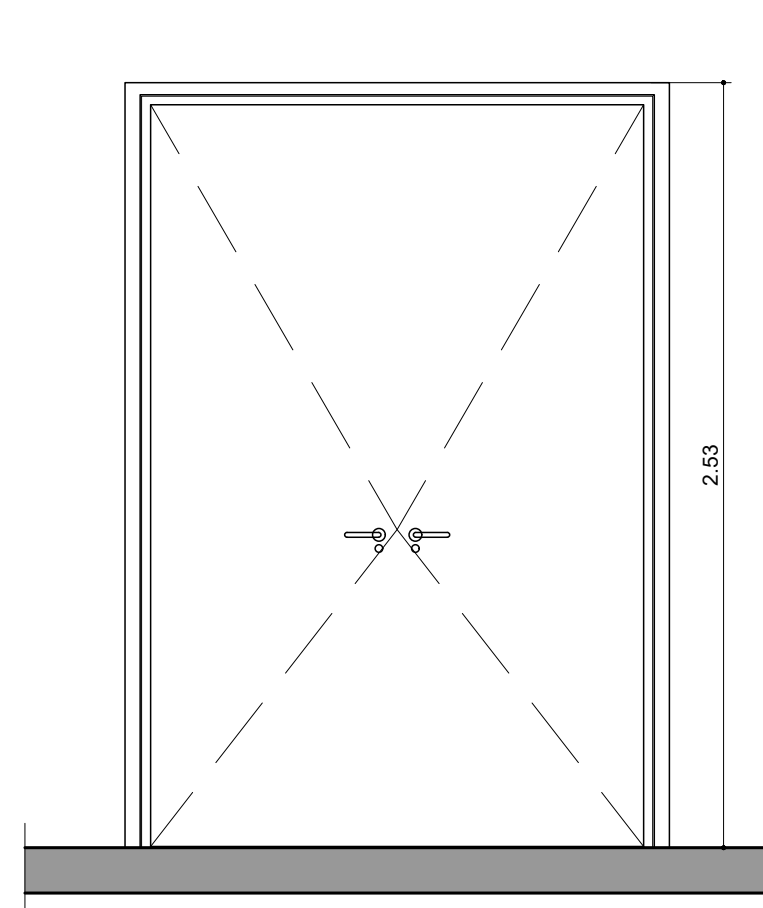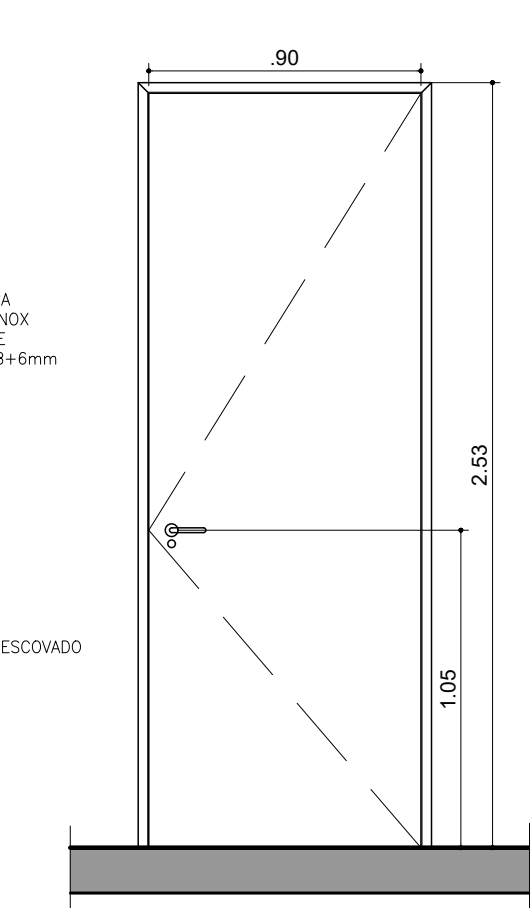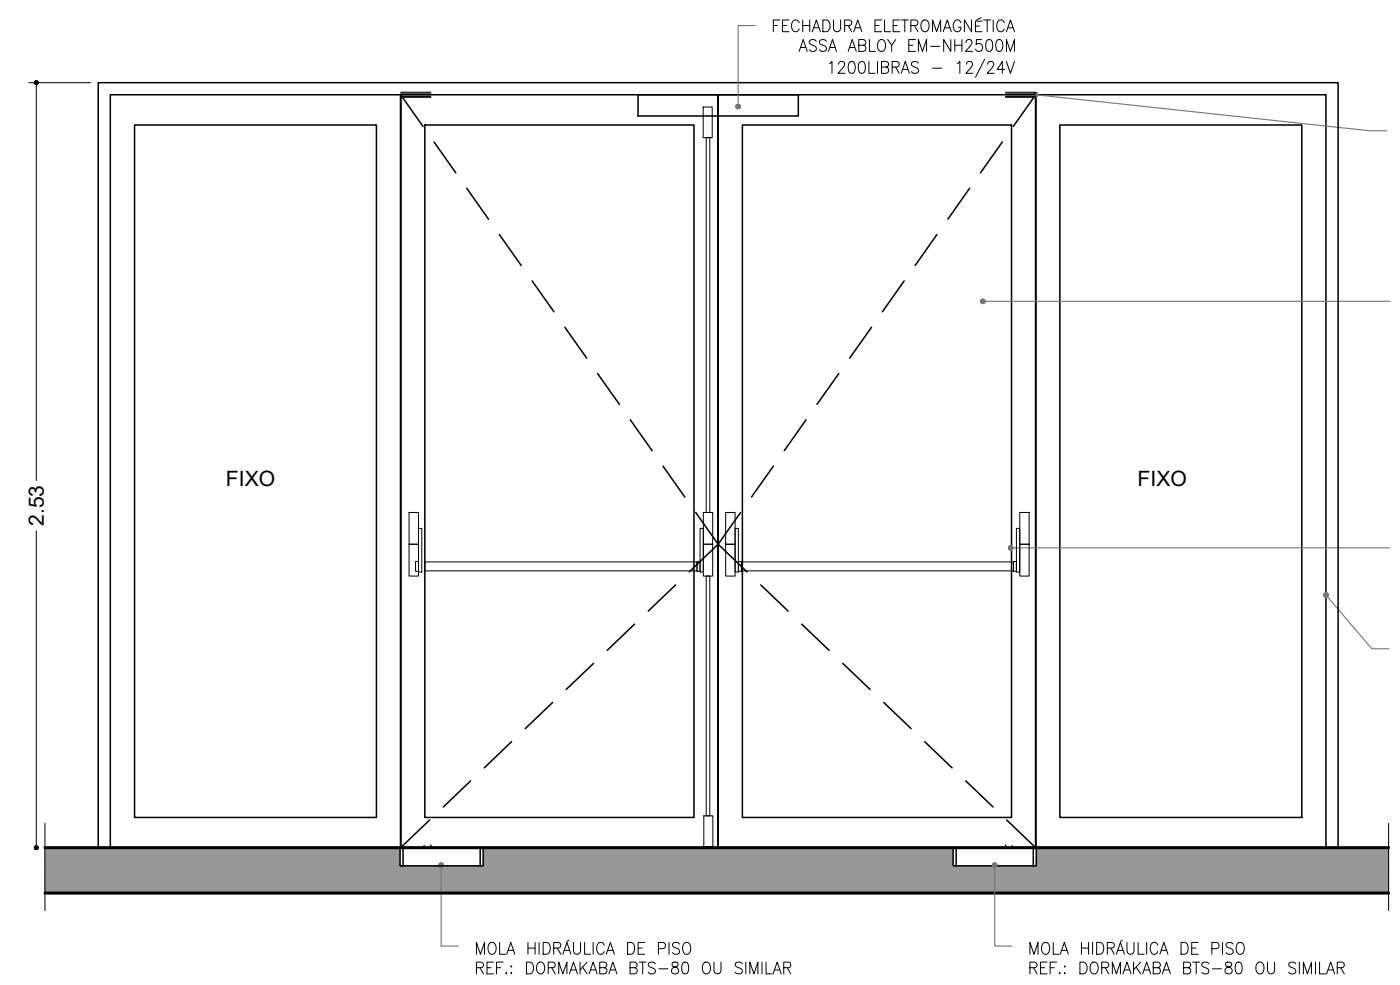


**1 PVD-M1**  
01 UNIDADE – PORTA DE VIDRO DE SEGURANÇA C/ BARRA ANTI-PÂNICO E FECHADURA MATERIAL: AÇO CARBONO ASTM 36 – 2mm ACABAMENTO INOX ESCOVADO E VIDRO 12mm (6mm + PVB + 6mm) FECHADURA ELETROMAGNÉTICA ACIONADA REMOTAMENTE

**2 PME-M2**  
01 UNIDADE – PORTA SIMPLES SEGURANÇA MATERIAL: CHAPA DE AÇO CARBONO ASTM 36 – 2mm – PINTADO COR PRETA


**3 PME-M3**  
02 UNIDADES – PORTA DUPLA SEGURANÇA MATERIAL: CHAPA DE AÇO CARBONO ASTM 36 – 2mm – PINTADO COR PRETA

**7 PVD-P1**  
02 UNIDADES – PORTA DE VIDRO DE SEGURANÇA C/ BARRA ANTI-PÂNICO E FECHADURA MATERIAL: AÇO CARBONO ASTM 36 – 2mm ACABAMENTO INOX ESCOVADO E VIDRO 12mm (6mm + PVB + 6mm) FECHADURA ELETROMAGNÉTICA ACIONADA REMOTAMENTE


**8 PVD-P2**  
02 UNIDADES – PORTA DE VIDRO DE SEGURANÇA C/ BARRA ANTI-PÂNICO E FECHADURA MATERIAL: AÇO CARBONO ASTM 36 – 2mm ACABAMENTO INOX ESCOVADO E VIDRO 12mm (6mm + PVB + 6mm) FECHADURA ELETROMAGNÉTICA ACIONADA REMOTAMENTE

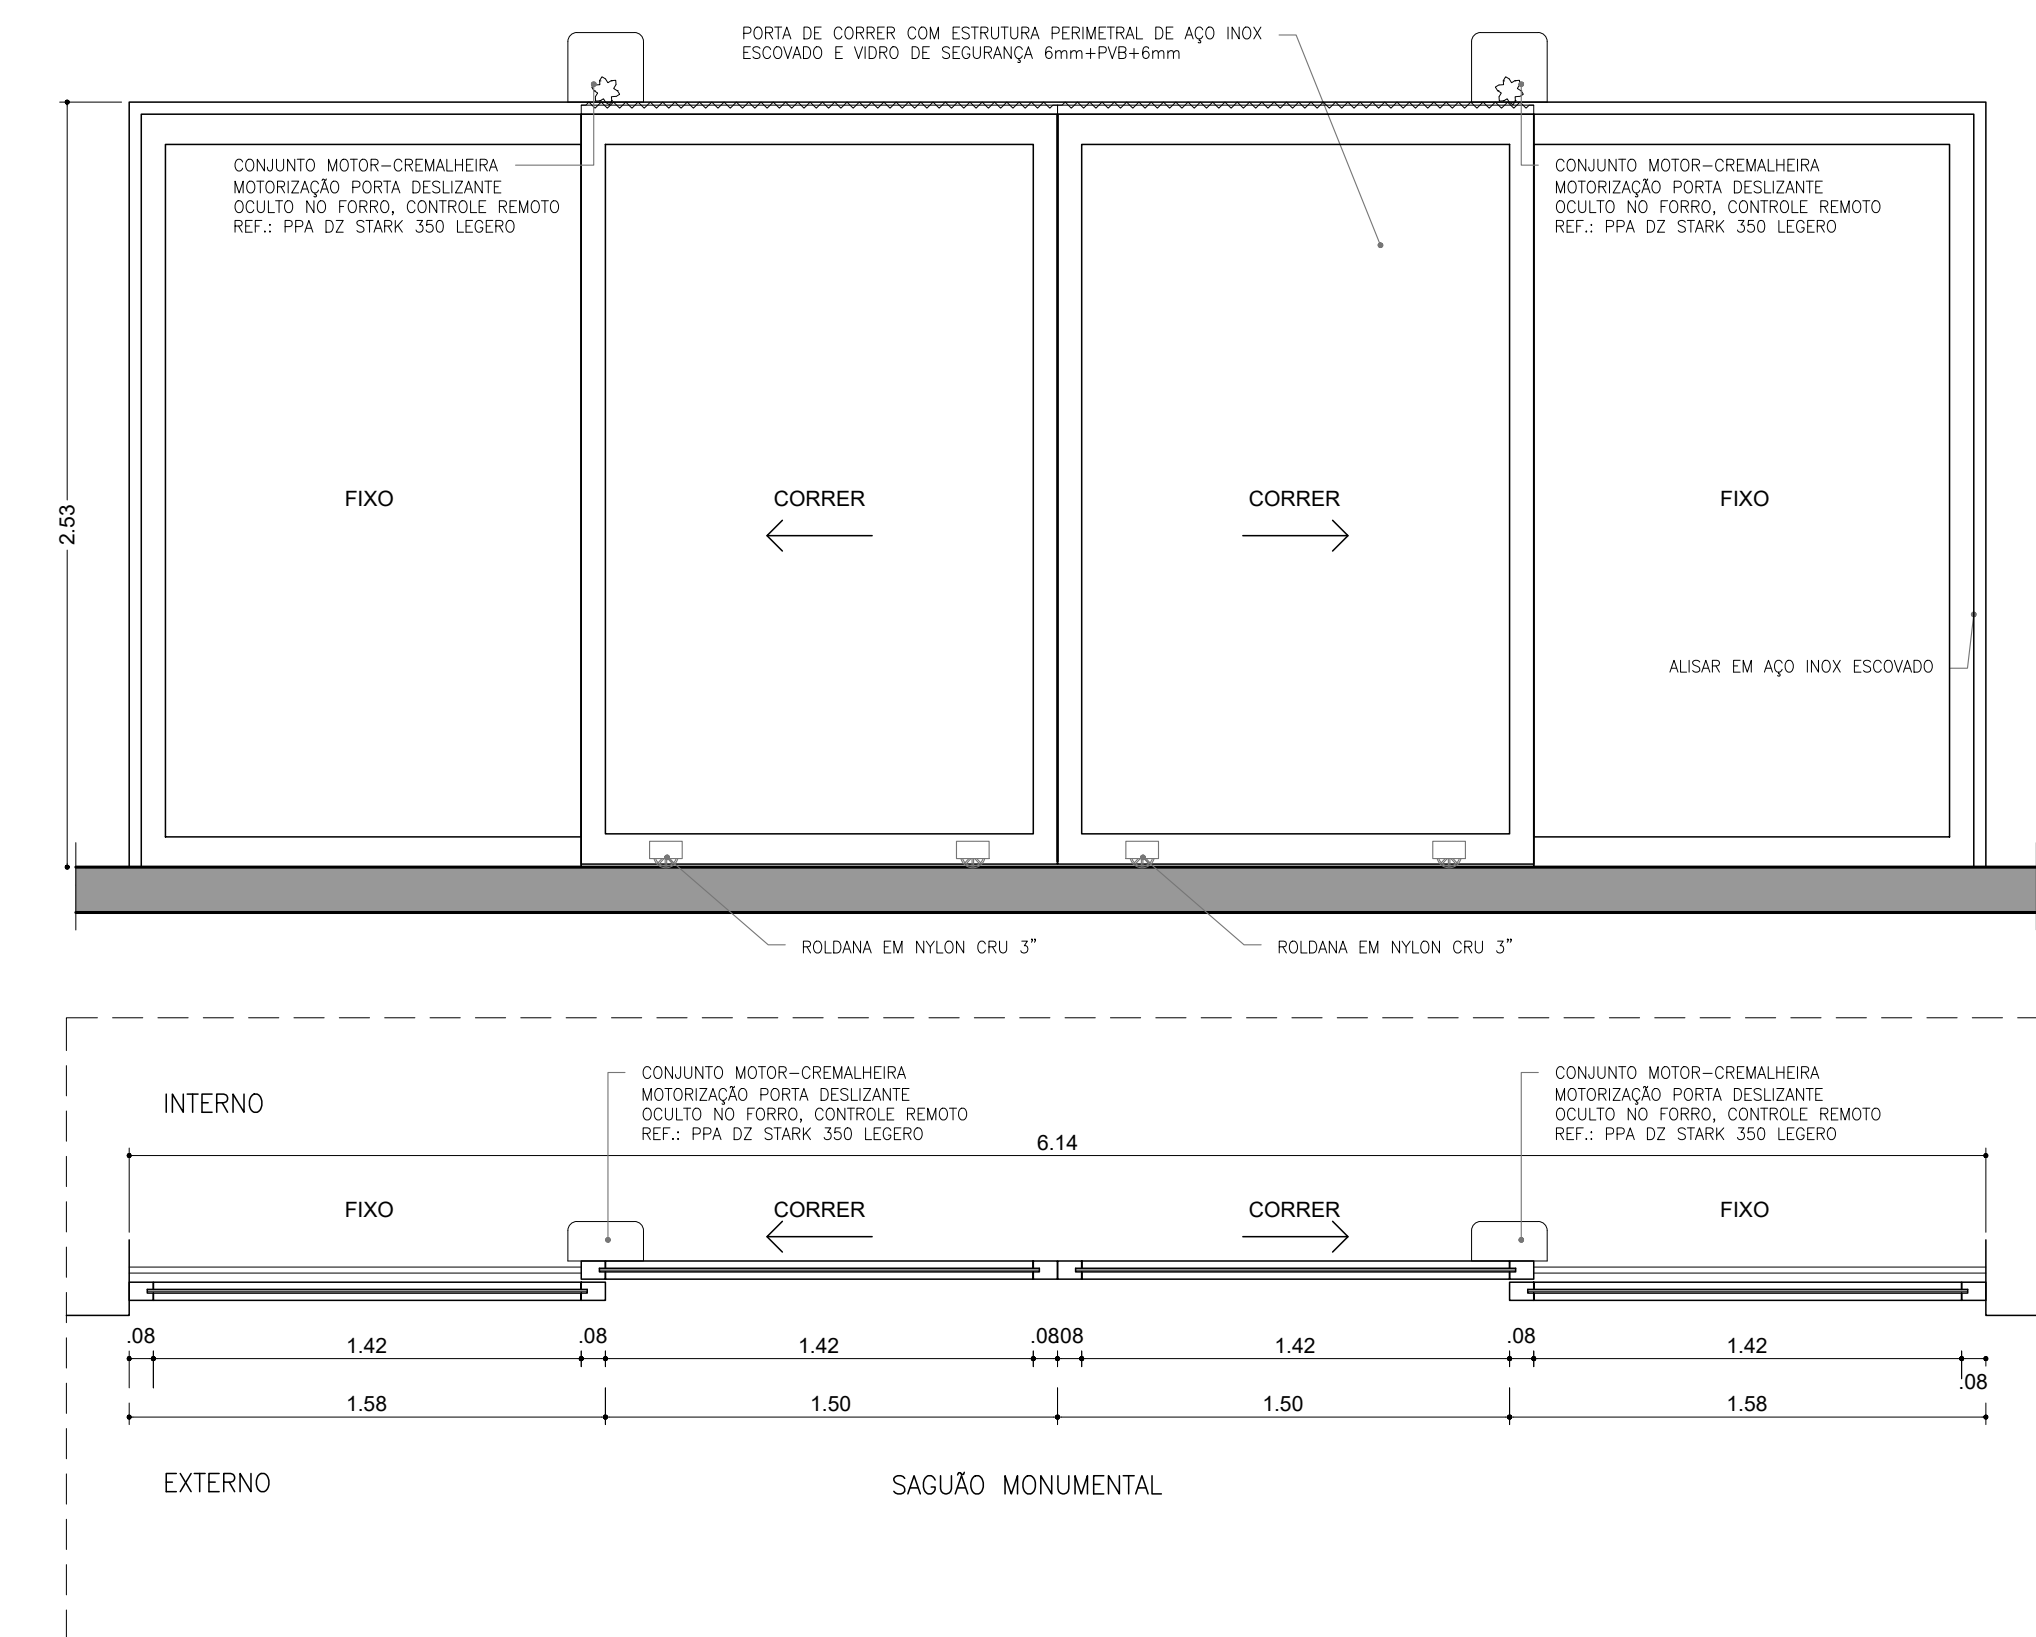

**4 PVD-T1**  
01 UNIDADE – PORTA DESLIZANTE DE VIDRO DE SEGURANÇA C/ MOTOR E CREMALHEIRA ACIONAMENTO REMOTO MATERIAL: AÇO CARBONO ASTM 36 – 2mm ACABAMENTO INOX ESCOVADO E VIDRO 12mm (6mm + PVB + 6mm) FECHADURA ELETROMAGNÉTICA ACIONADA REMOTAMENTE

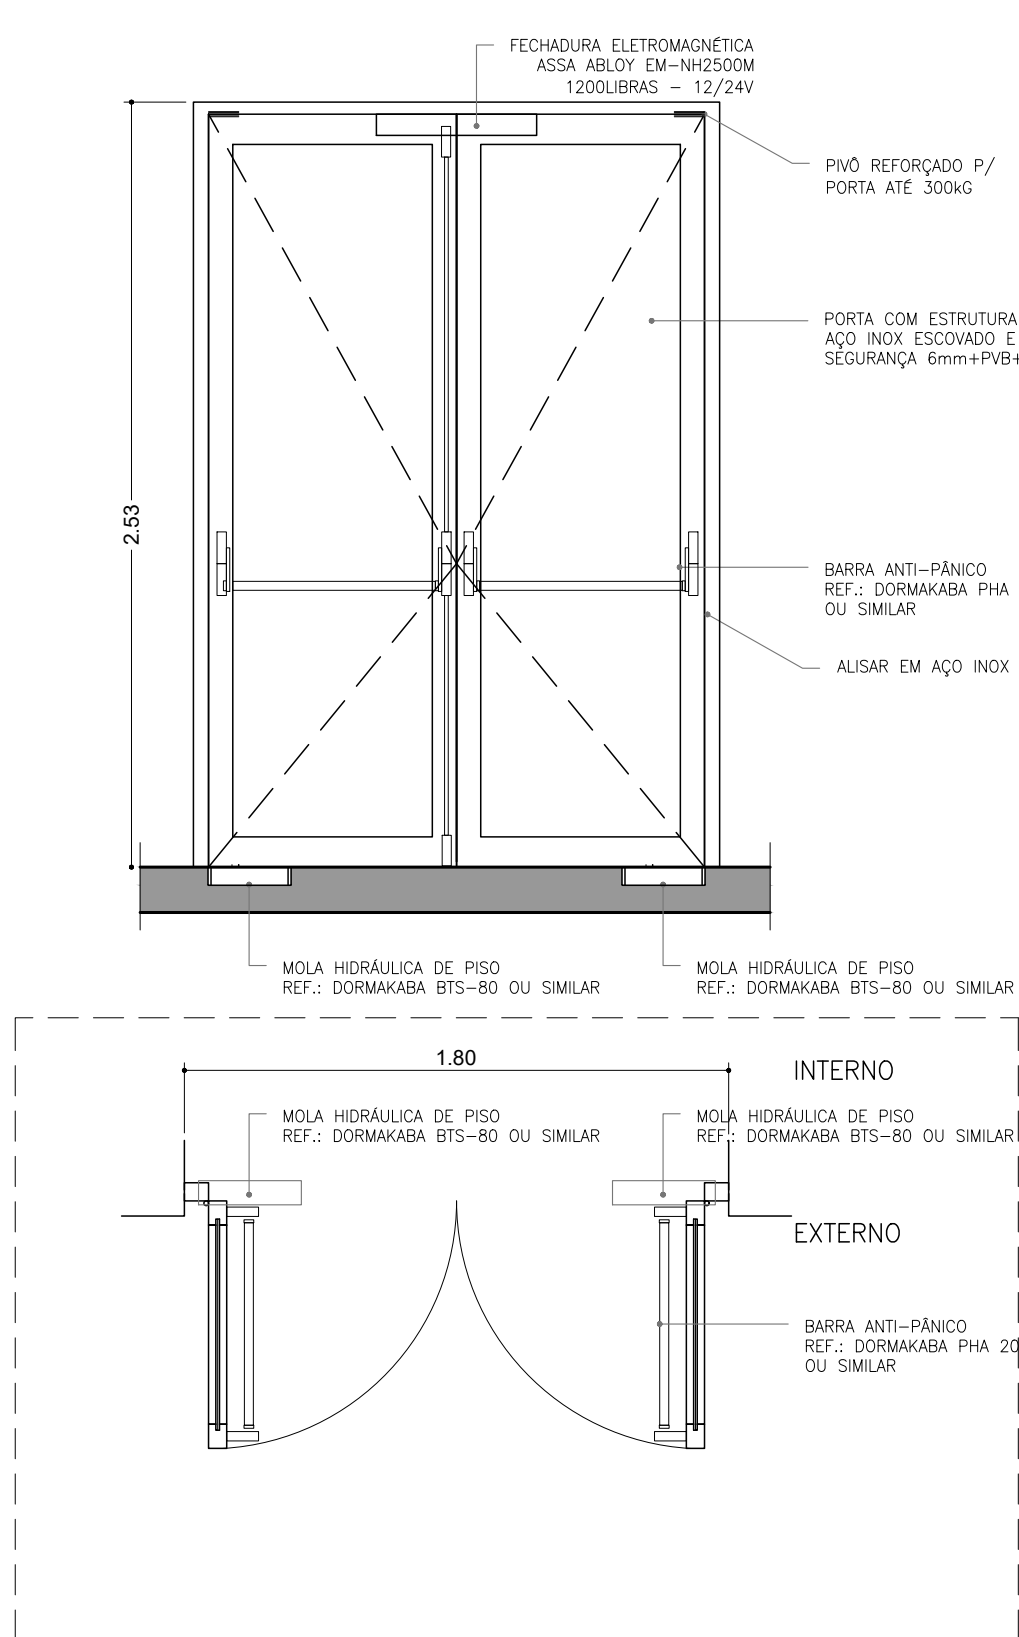

**5 PVD-T2**  
02 UNIDADES – PORTA DE VIDRO DE SEGURANÇA C/ BARRA ANTI-PÂNICO E FECHADURA MATERIAL: AÇO CARBONO ASTM 36 – 2mm ACABAMENTO INOX ESCOVADO E VIDRO 12mm (6mm + PVB + 6mm) FECHADURA ELETROMAGNÉTICA ACIONADA REMOTAMENTE

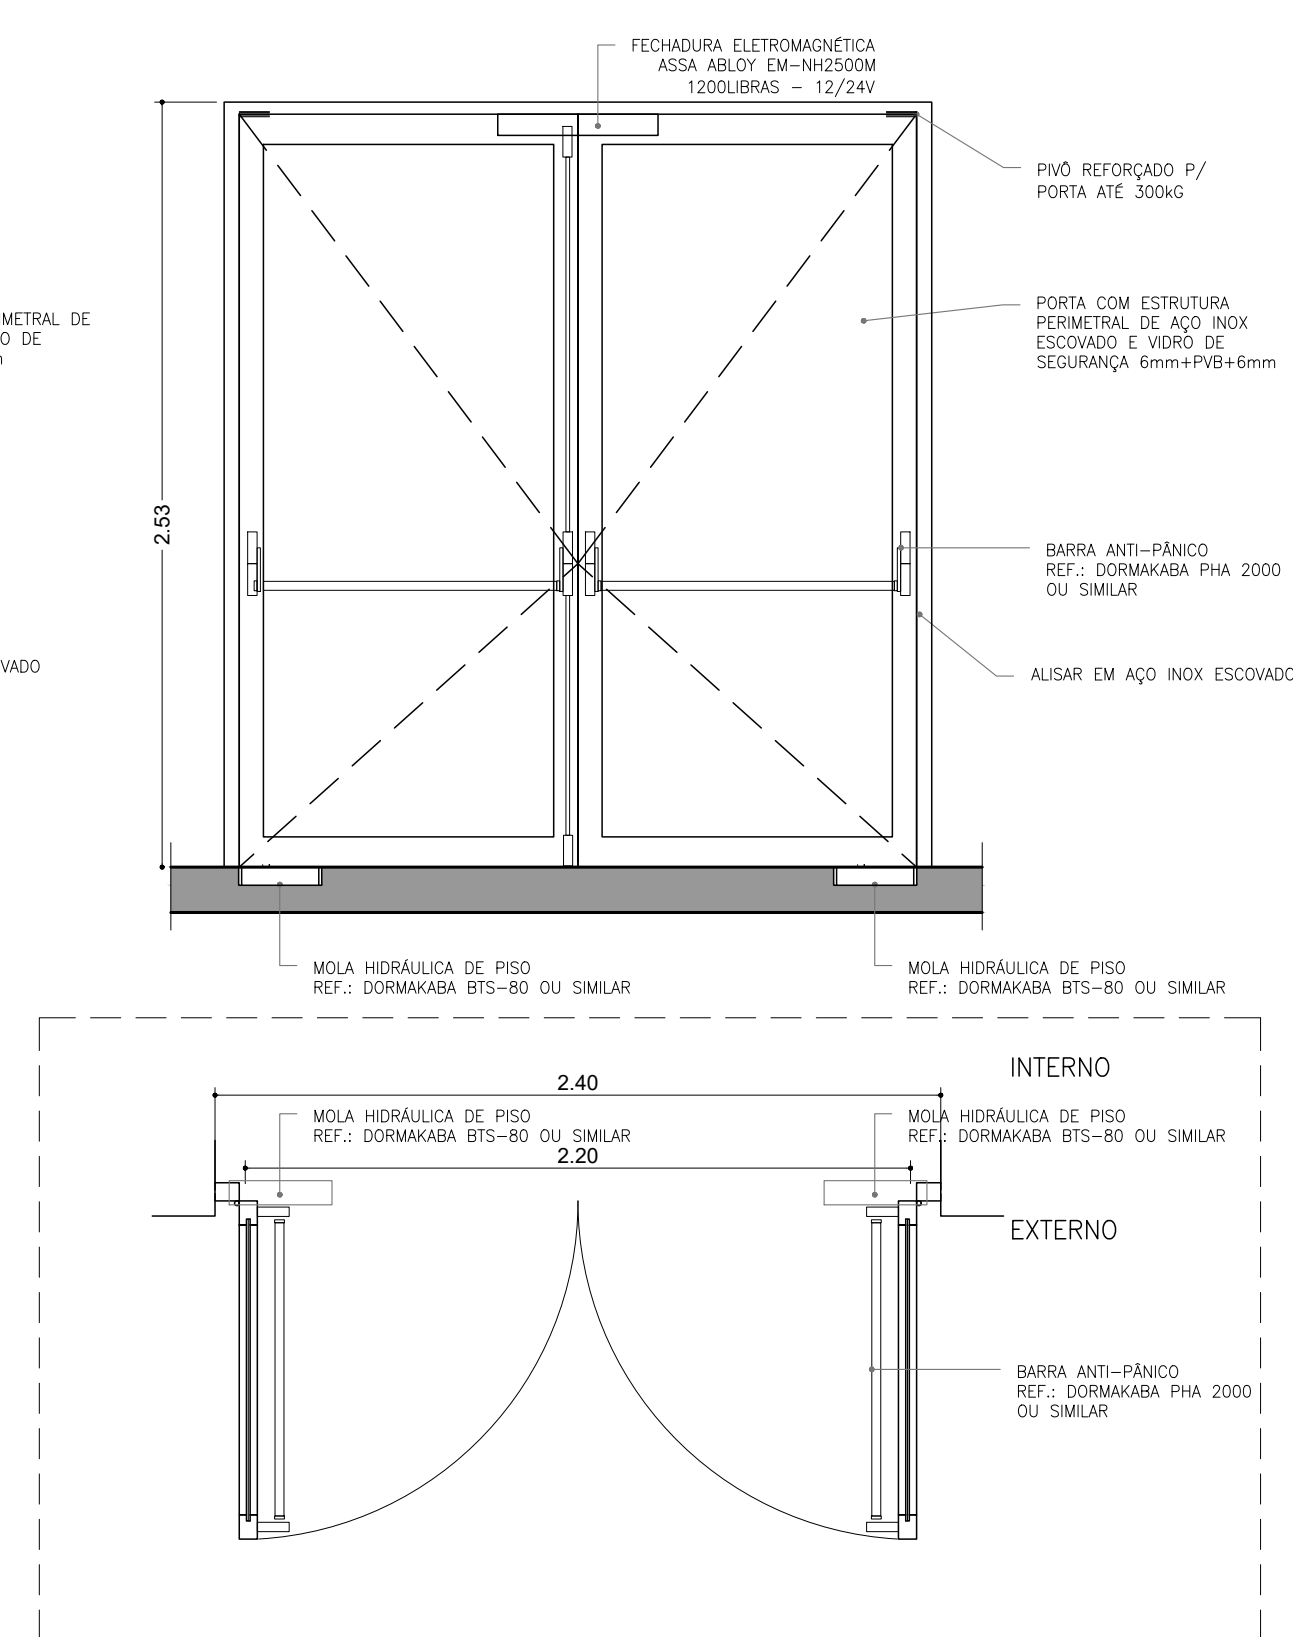


**6 PVD-T3**  
01 UNIDADE – PORTA DE VIDRO DE SEGURANÇA C/ BARRA ANTI-PÂNICO E FECHADURA MATERIAL: AÇO CARBONO ASTM 36 – 2mm ACABAMENTO INOX ESCOVADO E VIDRO 12mm (6mm + PVB + 6mm) FECHADURA ELETROMAGNÉTICA ACIONADA REMOTAMENTE

| TABELA DE PORTAS DE SEGURANÇA |            |        |    |           |   |
|-------------------------------|------------|--------|----|-----------|---|
| ITEM                          | PAVIMENTO  | CODIGO | QT | DIMENSÕES | DESCRIÇÃO   |
| 1                             | MONUMENTAL | PVD-M1 | 1  | 4,09X2,53 | PORTA DUPLA PIVOTANTE E DUAS PARTES FIXAS - VIDRO DE SEGURANÇA C/ BARRA ANTI-PANICO E FECHADURA MATERIAL: AÇO CARBONO ASTM 36 - 2mm ACABAMENTO INOX ESCOVADO E VIDRO TEMPERADO E LAMINADO 12mm (6mm + PVB + 6mm)                           |
| 2                             | MONUMENTAL | PME-M2 | 1  | 0,9X2,53  | PORTA DE SEGURANÇA SIMPLES DE GIRO MATERIAL: CHAPA DE AÇO CARBONO ASTM 36 - 2mm - PINTADO COR PRETA   |
| 3                             | MONUMENTAL | PME-M3 | 2  | 1,8X2,53  | PORTA DE SEGURANÇA DUPLA DE GIRO MATERIAL: CHAPA DE AÇO CARBONO ASTM 36 - 2mm - PINTADO COR PRETA   |
| 4                             | TERREO     | PVD-T1 | 1  | 6,14X2,53 | PORTA DESLIZANTE (DUAS FOLHAS MÓVEIS E DUAS FOLHAS FIXAS) DE VIDRO DE SEGURANÇA C/ MOTOR E CREMALHEIRA ACIONAMENTO REMOTO MATERIAL: AÇO CARBONO ASTM 36 - 2mm ACABAMENTO INOX ESCOVADO E VIDRO TEMPERADO E LAMINADO 12mm (6mm + PVB + 6mm) |
| 5                             | TERREO     | PVD-T2 | 2  | 1,8X2,53  | PORTA DUPLA PIVOTANTE - VIDRO DE SEGURANÇA C/ BARRA ANTI-PANICO E FECHADURA MATERIAL: AÇO CARBONO ASTM 36 - 2mm ACABAMENTO INOX ESCOVADO E VIDRO TEMPERADO E LAMINADO 12mm (6mm + PVB + 6mm)                                               |
| 6                             | TERREO     | PVD-T3 | 1  | 2,4X2,53  | PORTA DUPLA PIVOTANTE - VIDRO DE SEGURANÇA C/ BARRA ANTI-PANICO E FECHADURA MATERIAL: AÇO CARBONO ASTM 36 - 2mm ACABAMENTO INOX ESCOVADO E VIDRO TEMPERADO E LAMINADO 12mm (6mm + PVB + 6mm)                                               |
| 7                             | 1.PAV      | PVD-P1 | 2  | 1,6X2,53  | PORTA DUPLA PIVOTANTE - VIDRO DE SEGURANÇA C/ BARRA ANTI-PANICO E FECHADURA MATERIAL: AÇO CARBONO ASTM 36 - 2mm ACABAMENTO INOX ESCOVADO E VIDRO TEMPERADO E LAMINADO 12mm (6mm + PVB + 6mm)                                               |
| 8                             | 1.PAV      | PVD-P2 | 2  | 2,4X2,53  | PORTA DUPLA PIVOTANTE - VIDRO DE SEGURANÇA C/ BARRA ANTI-PANICO E FECHADURA MATERIAL: AÇO CARBONO ASTM 36 - 2mm ACABAMENTO INOX ESCOVADO E VIDRO TEMPERADO E LAMINADO 12mm (6mm + PVB + 6mm)                                               |

NOTA: CONFERIR MEDIDAS NA OBRA  
NOTA: DIMENSÕES DO VÃO TOTAL  
ATENDER AS NORMAS:  
NBR 7199 – VIDROS NA CONSTRUÇÃO CIVIL  
NBR 14697 – VIDRO LAMINADO  
NBR 8800 – CÁLCULO E EXECUÇÃO DE ESTRUTURAS DE AÇO  
NBR 6123 – FORÇAS DEVIDAS AO VENTO EM EDIFICAÇÕES  
NBR 6120 – CARGAS PARA CALCULO DE ESTRUTURA EM EDIFICAÇÕES  
AISC – AMERICAN INSTITUTE OF STEEL CONSTRUCTIONS  
AWS – AMERICAN WELDING SOCIETY AISI – AMERICAN IRON AND STEEL INSTITUTE.

OBSERVAÇÕES  
1- AS FECHADURAS MAGNÉTICAS SERÃO CONTROLADAS PELA CENTRAL DE CFTV SALA S67 SUBSOLO



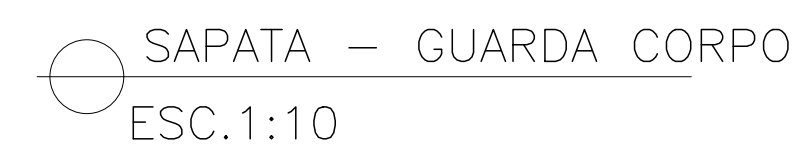

ATENDER AS NORMAS:  
 NBR 7199 – VIDROS NA CONSTRUÇÃO CIVIL  
 NBR 14697 – VIDRO LAMINADO  
 NBR 8800 – CÁLCULO E EXECUÇÃO DE ESTRUTURAS DE AÇO  
 NBR 6123 – FORÇAS DEVIDAS AO VENTO EM EDIFICAÇÕES  
 NBR 6120 – CARGAS PARA CÁLCULO DE ESTRUTURA EM EDIFICAÇÕES  
 AISI – AMERICAN INSTITUTE OF STEEL CONSTRUCTIONS  
 AWS – AMERICAN WELDING SOCIETY  
 AISI – AMERICAN IRON AND STEEL INSTITUTE.

|             |  |
|-------------|--|
| OBSERVAÇÕES |  |
|-------------|--|





OBSERVAÇÕES